


PROJETOS
EXECUTIVOS

BUILDING INFORMATION MODELING

CADERNO DE PROJETOS - BIM

ARQUITETURA | ESTRUTURA | ELÉTRICA | HIDRÁULICA

ELABORADO POR
NATANAEL MENEZES

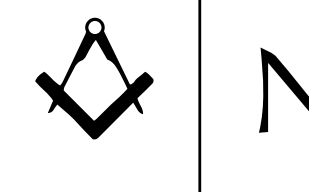

SOBRE O CADERNO DE PROJETOS


O que será apresentado neste caderno?

É um caderno com todos os projetos executivos de uma edificação residencial onde foi elaborado o modelo em BIM e extraído todas as pranchas técnicas e quantitativos para execução da Obra. Além disso foi feito a compatibilização das disciplinas de projetos para análise das interferências.





AutoCAD 2d
Revit Architecture

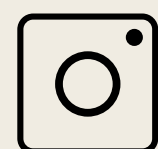

@arq.natann



N

AUTOR

Natanael Menezes

Estudante de arquitetura e urbanismo.

Cursando atualmente o 7º semestre.

Faculdade: Unicid – Universidade Cidade de São Paulo.

Data de conclusão: 01/12/2024

•Cursos:

Informática básica – Senai Luis Eulalio de Bueno Vidigal Filho

Automação hidráulica industrial – Senai Roberto Simonsen

Excel básico – Senai Hermenegildo Campos de Almeida


AutoCAD 2d – Senai Orlando Laviero Ferraiuolo

Revit Architecture – Senai Orlando Laviero Ferraiuolo

•Trabalha atualmente na empresa Rossetti, como assistente técnico.

•Experiência anteriores:


Projeto de arquitetura, instalações elétricas e hidráulicas. Desenvolvendo trabalhos para clientes externos

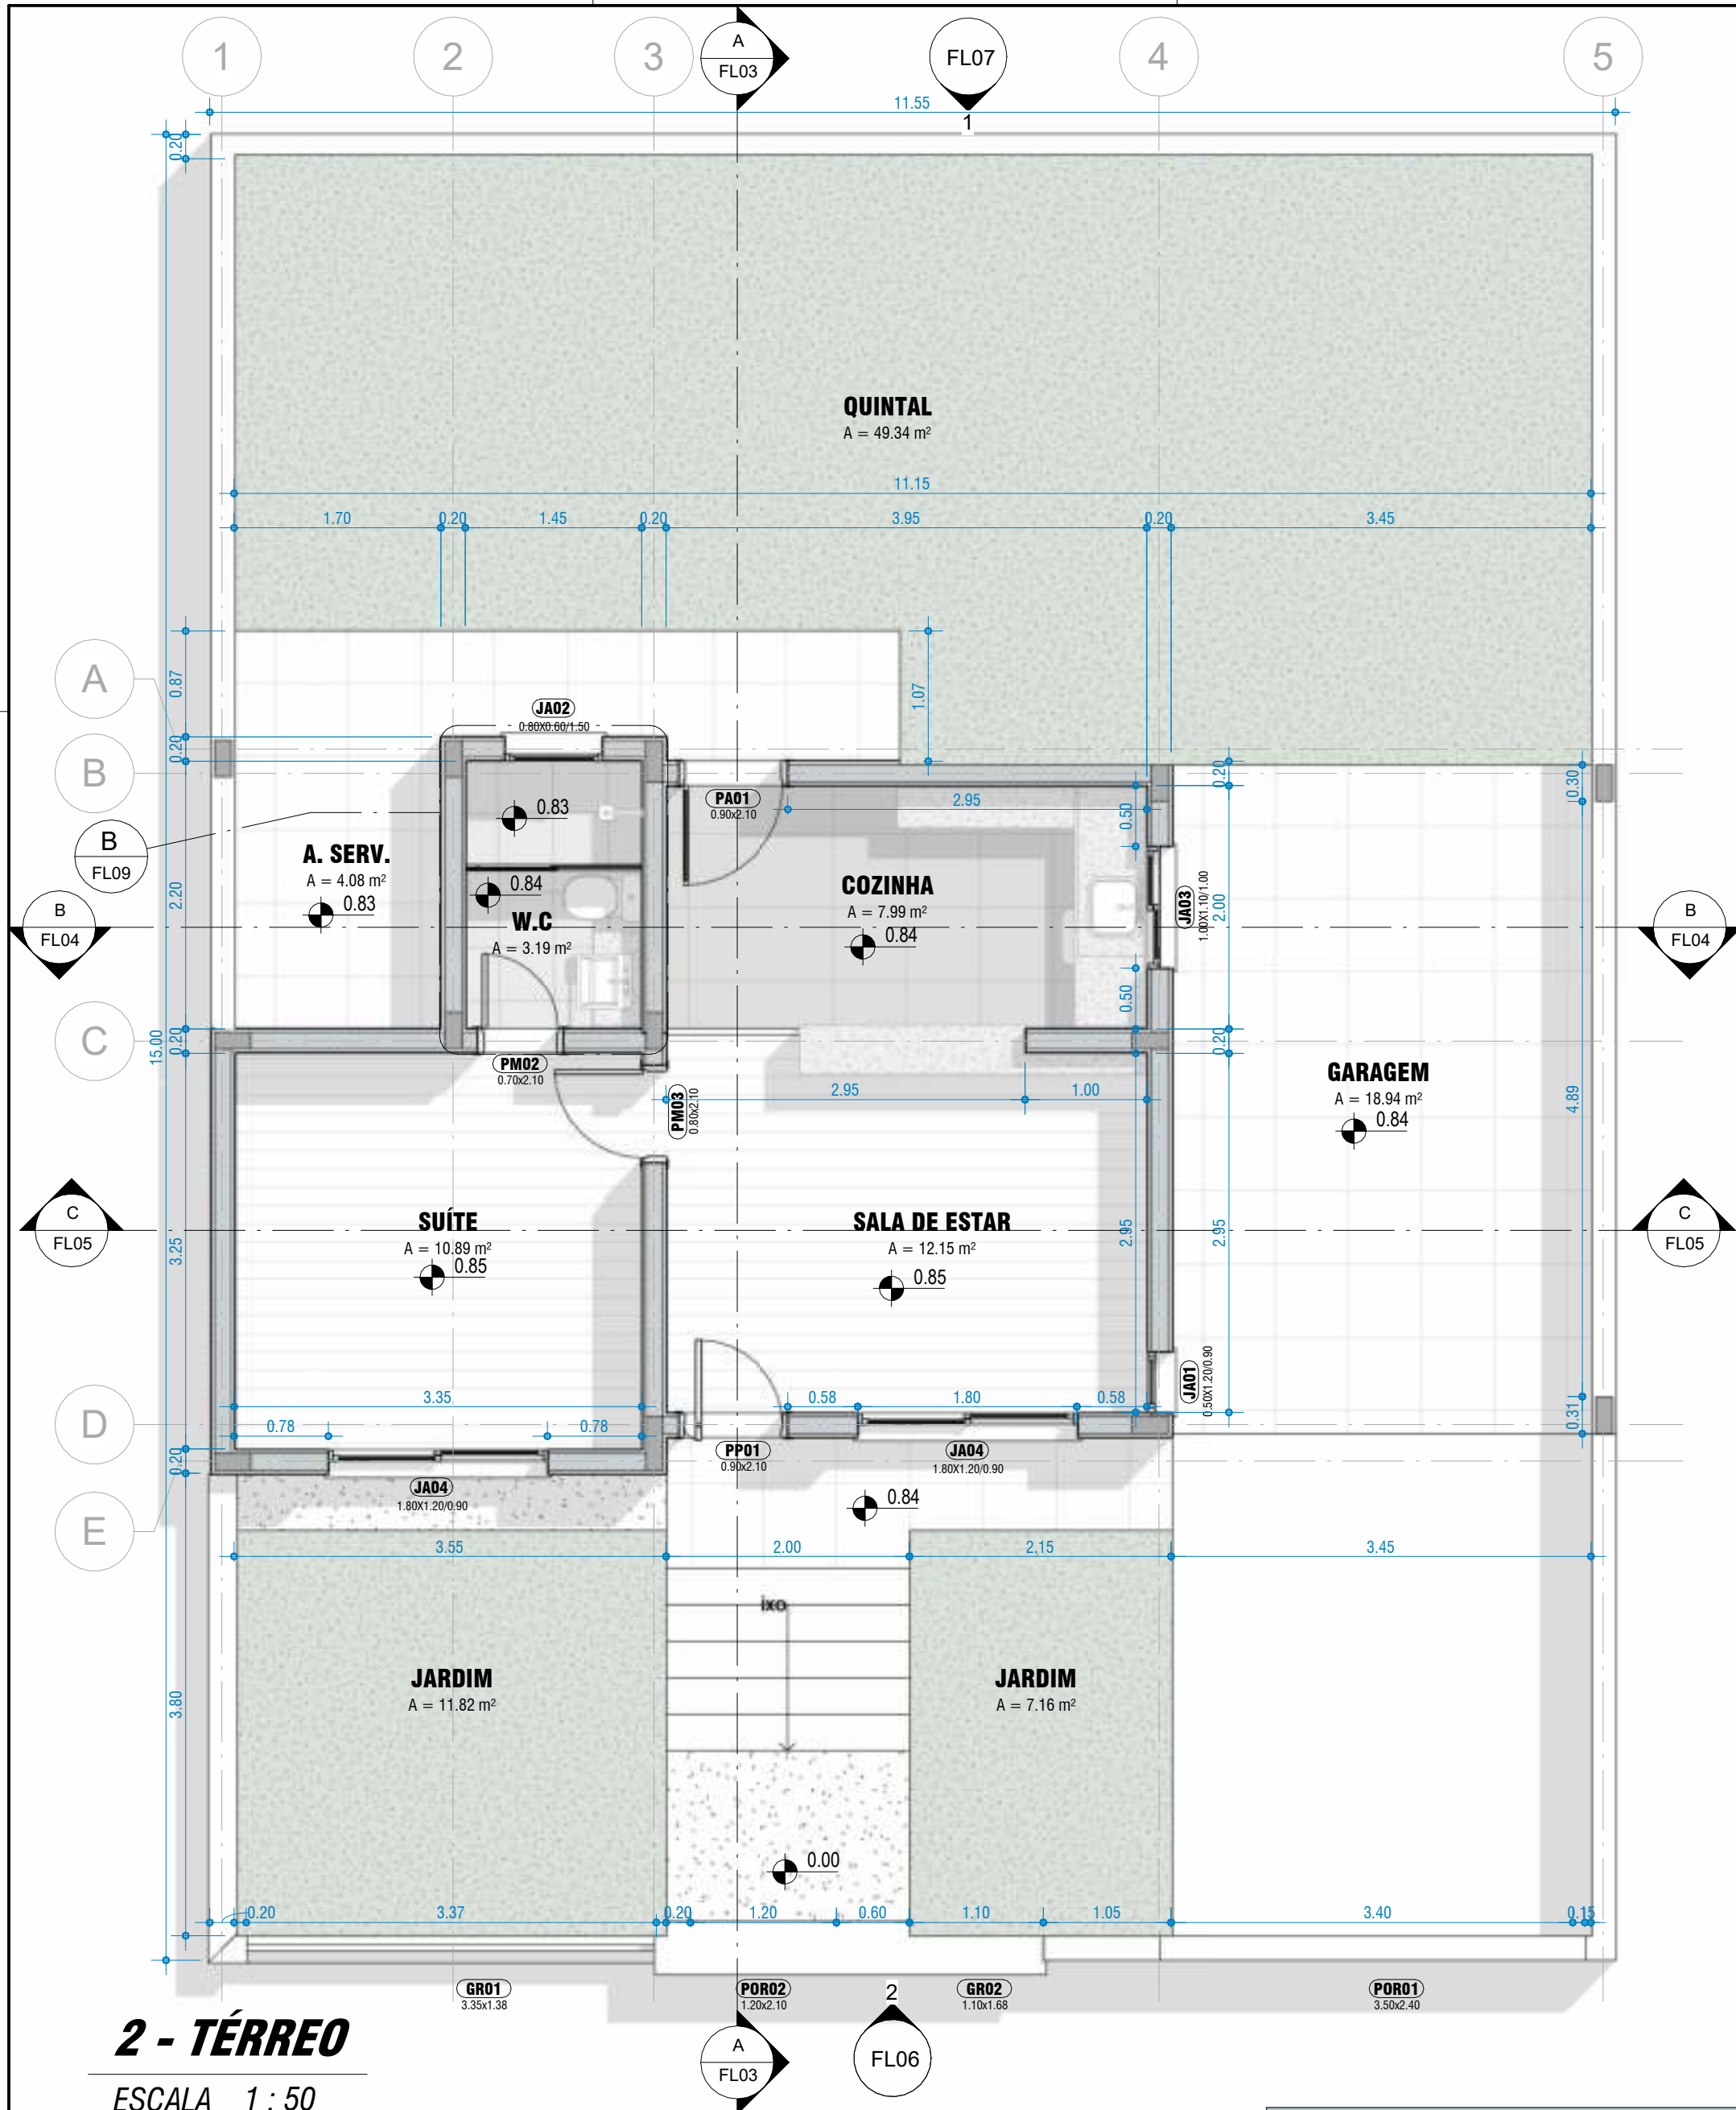

2 - TÉRREO
ESCALA 1 : 50

TABELA DE JANELAS					
QTD.	CÓD.	DESCRIÇÃO	LARG.	ALT.	PEIT ORIL
1	JA01	JANELA BASCULANTE + PEITORIL FIXO - VIDRO	0.50	1.20	0.90
1	JA02	JANELA MAXIM-AR	0.80	0.60	1.50
1	JA03	JANELA 2 FLS CORRER - VIDRO	1.00	1.10	1.00
2	JA04	JANELA 2 FLS CORRER - VIDRO	1.80	1.20	0.90

TABELA DE PORTAS				
QT D.	CÓD.	DESCRIÇÃO	LARG.	ALT.
1	PP01	PORTA PIVOTANTE - MADEIRA	0.90	2.10
1	PM03	PORTA DE GIRO - MADEIRA	0.80	2.10
1	PM02	PORTA DE GIRO - MADEIRA	0.70	2.10
1	PA01	PORTA DE GIRO - ALUMÍNIO + VIDRO	0.90	2.10

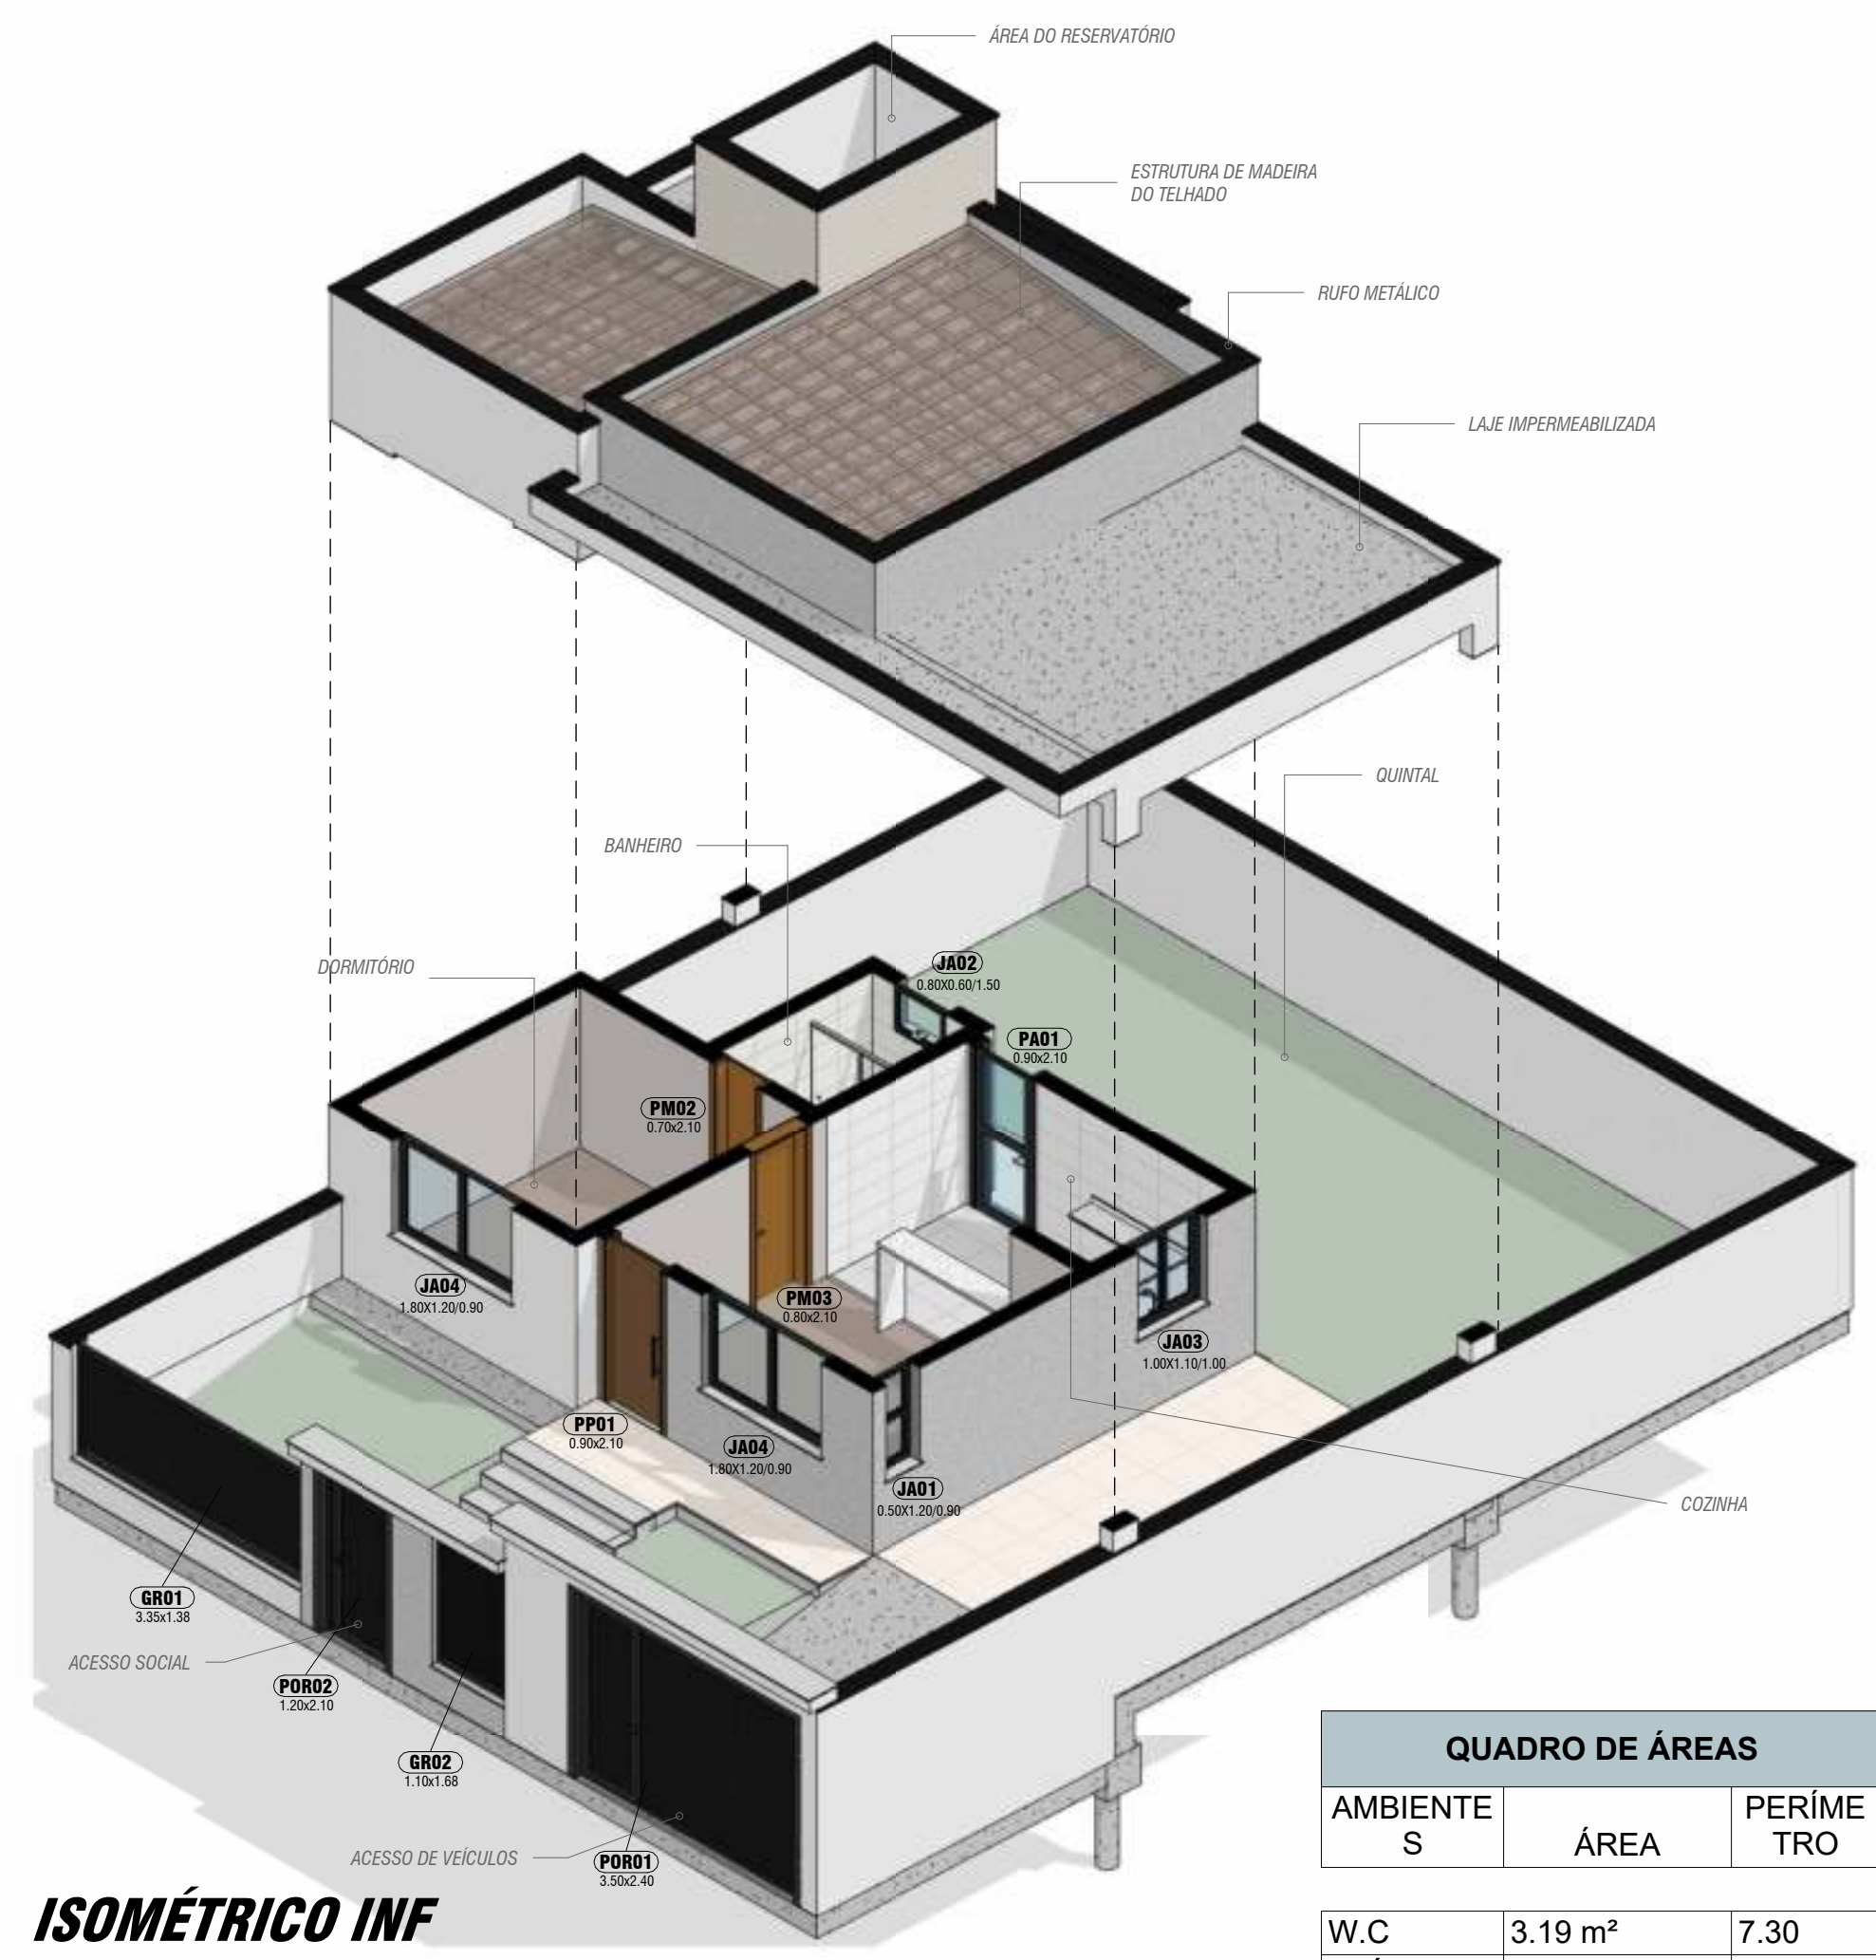

QUADRO DE ÁREAS		
AMBIENTE S	ÁREA	PERÍMETRO
W.C	3.19 m²	7.30
SUÍTE	10.89 m²	13.20
COZINHA	7.99 m²	11.93
SALA DE ESTAR	12.15 m²	14.14
GARAGEM	18.94 m²	17.88
A. SERV.	4.08 m²	8.20
QUINTAL	49.34 m²	32.20
JARDIM	7.16 m²	10.96
JARDIM	11.82 m²	13.76

NATANAEL MENEZES DA SILVA

TELEFONE: (11) 95135-5191
LOCALIZAÇÃO: SÃO PAULO

INSTAGRAM: athenas.arq

CONCEITO DO PROJETO:
APRESENTAÇÃO DE PORTFÓLIO




NOME DO PROJETO:
RESIDÊNCIA ATHENAS
TIPO DE PROJETO:
PROJETO ARQUITETÔNICO

DESENHADOR POR:
Natanael Menezes da Silva

APROVADO POR:
Natanael Menezes da Silva

DATA:
01/02/23
ESCALA:
1 : 75

FOLHA:
FL01
FORMATO:
A2

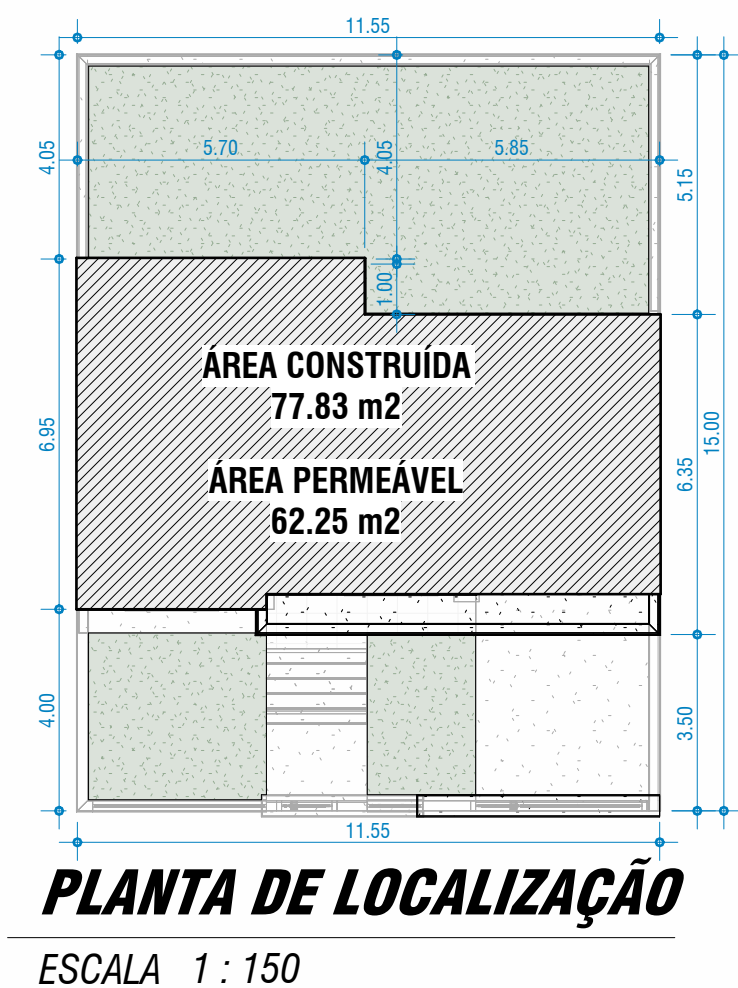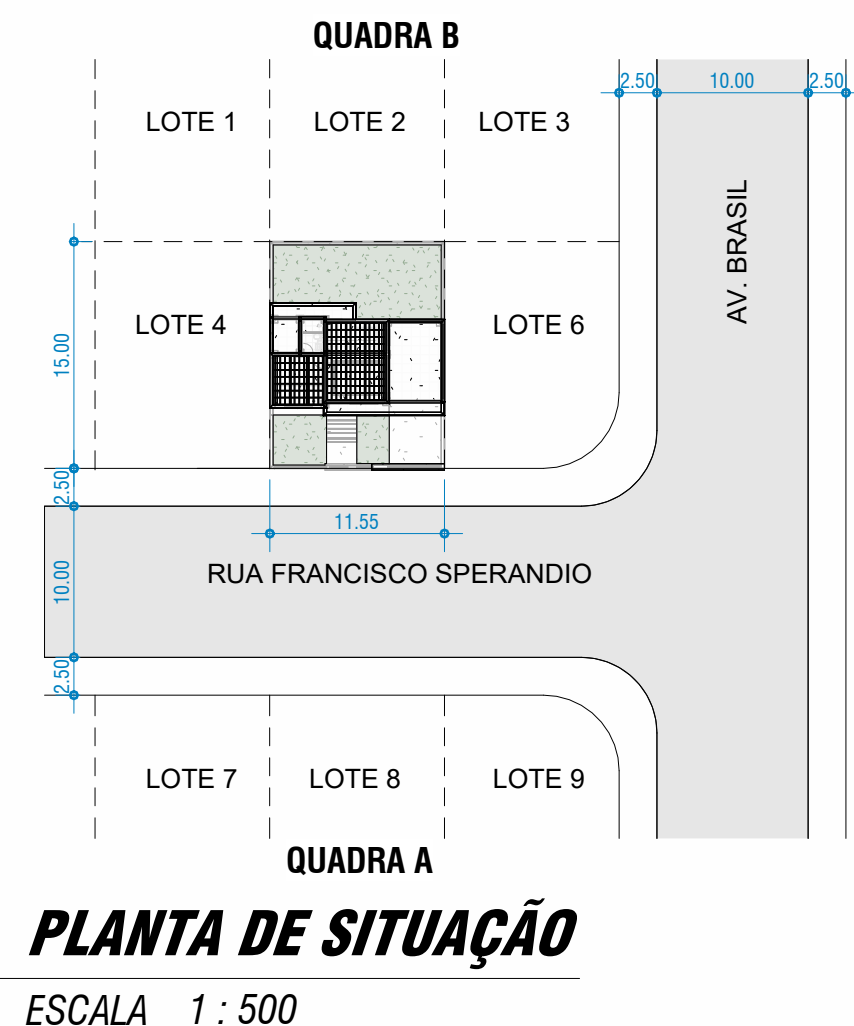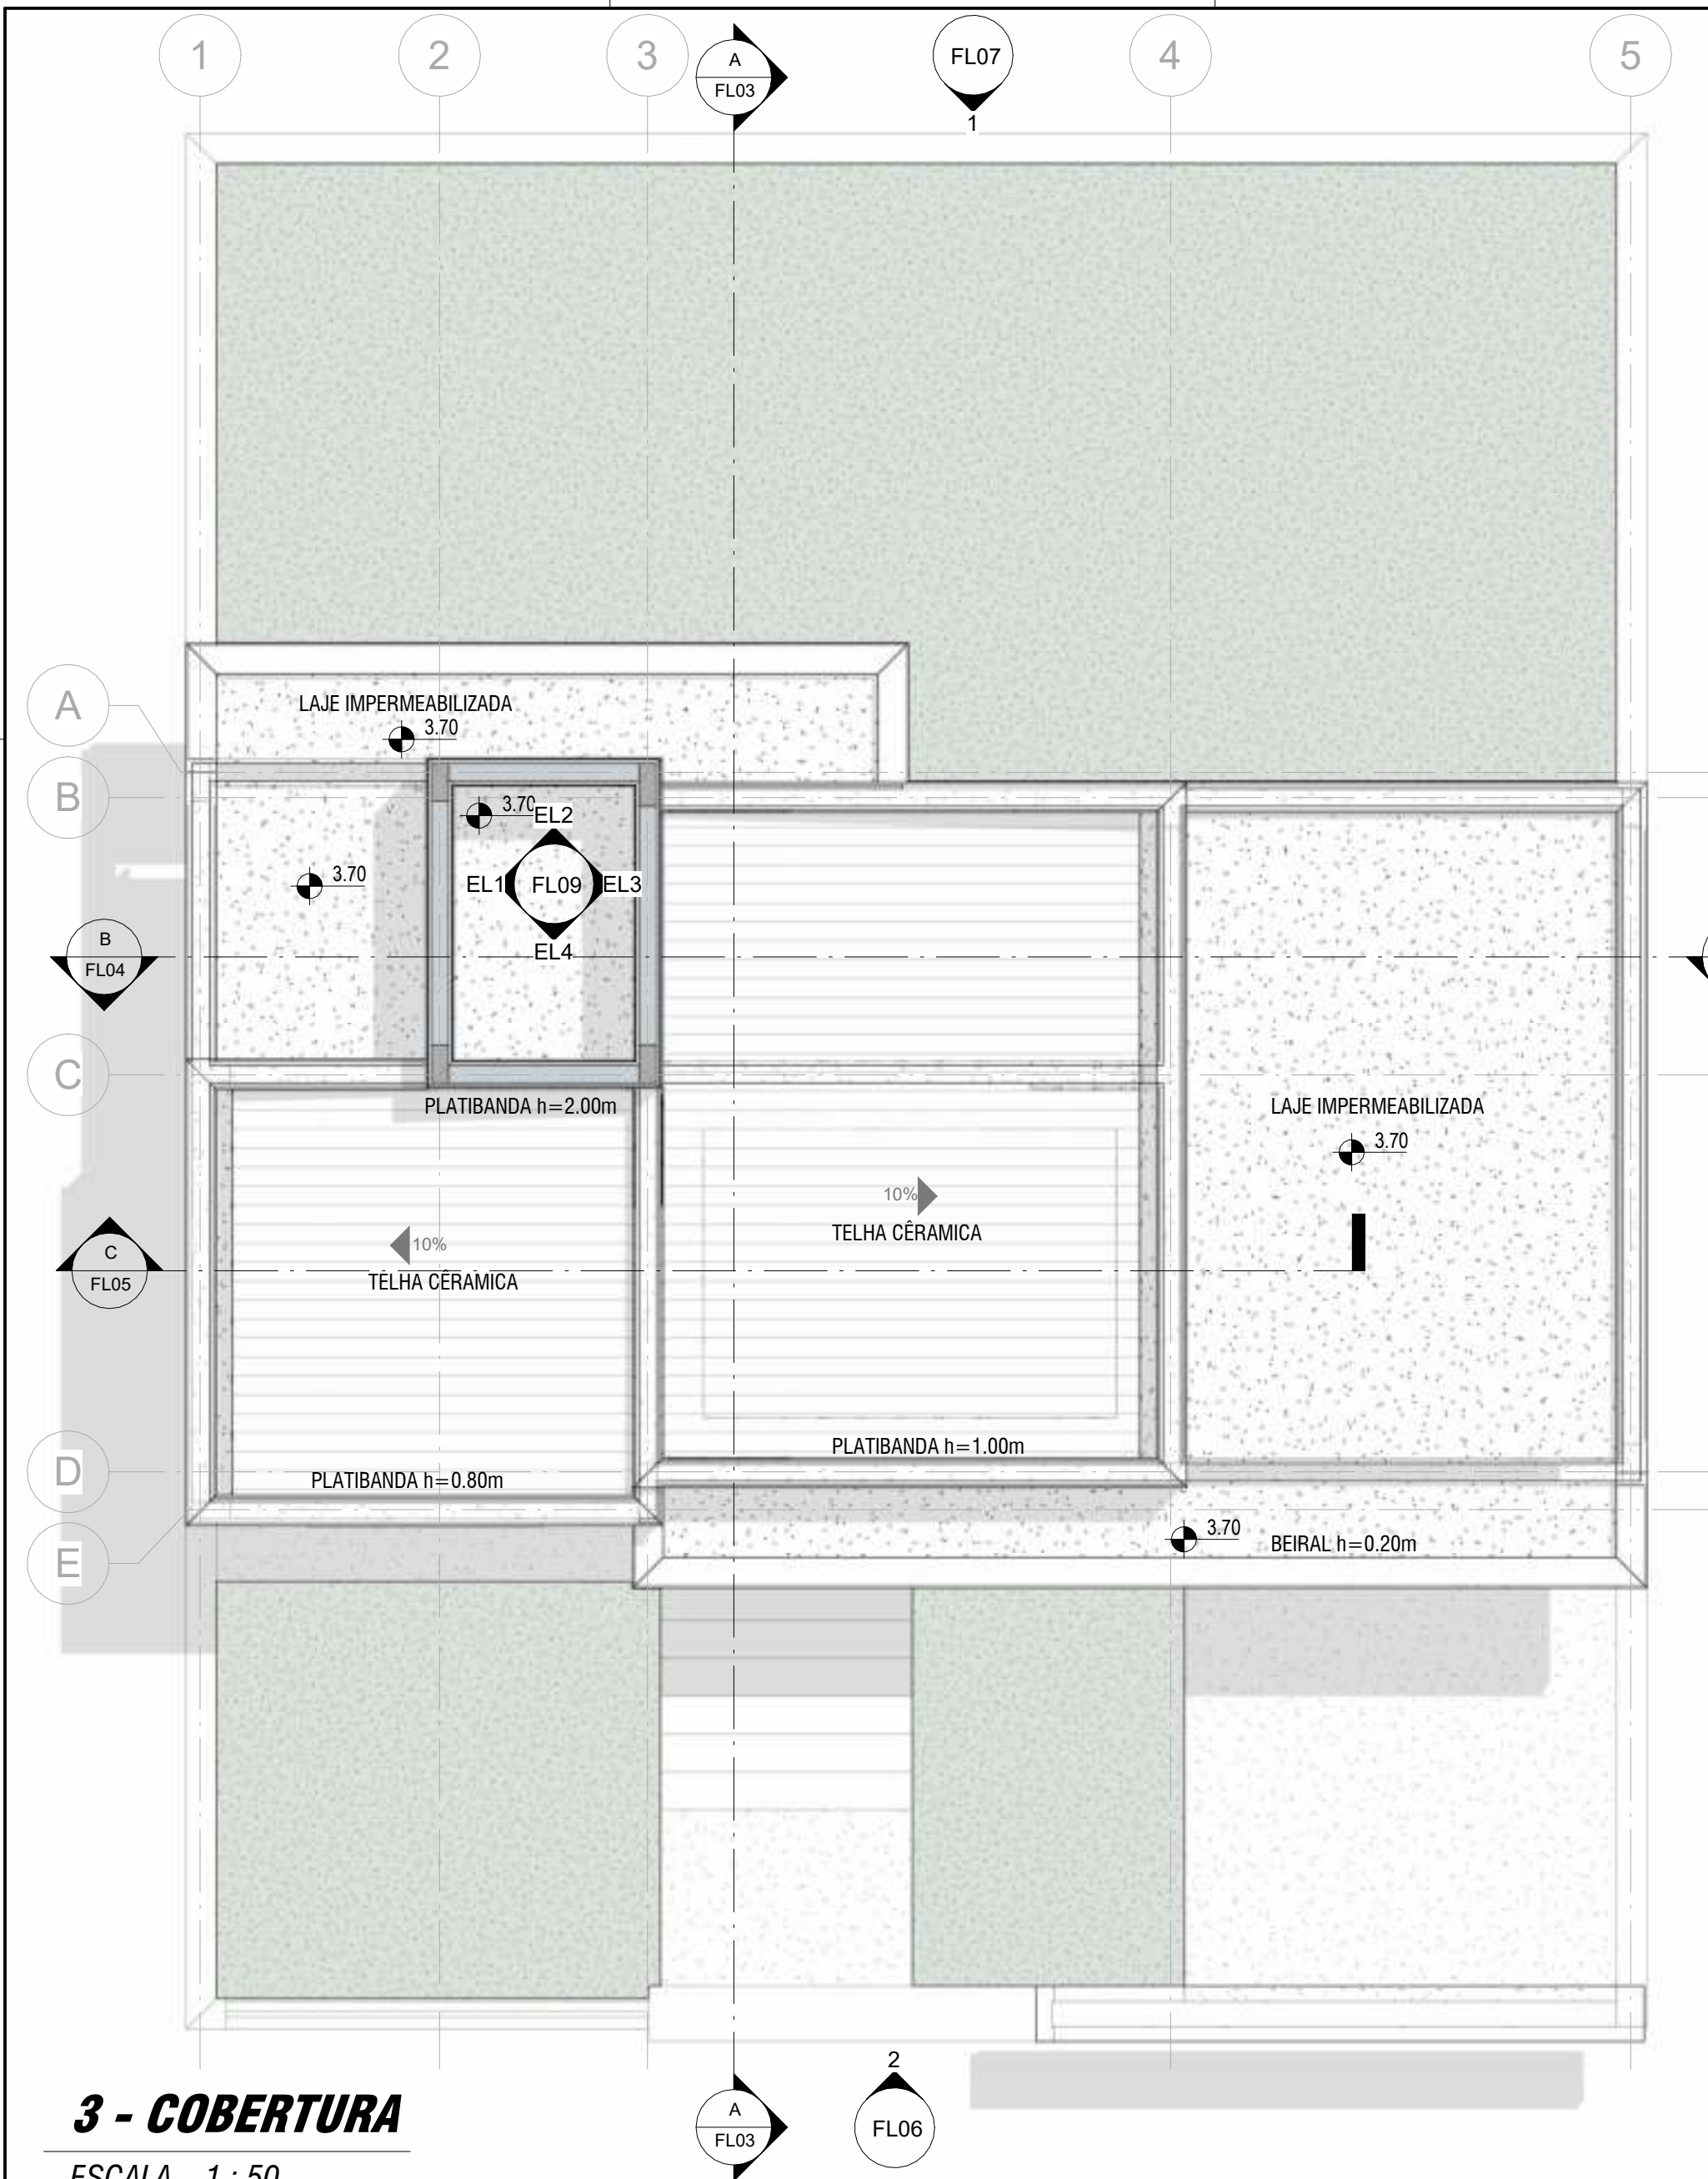

3 - COBERTURA
ESCALA 1 : 50

PLANTA DE SITUAÇÃO
ESCALA 1 : 500

PLANTA DE LOCALIZAÇÃO
ESCALA 1 : 150

QUANTITATIVO DE RUFOS	
Tipo	Comprimento
RUFO METALICO	102.50

QUANTITATIVO DE TELHAS	
DESCRIÇÃO	ÁREA (m²)
TELHAS	30.12 m²

NATANAEL MENEZES DA SILVA

TELEFONE: (11) 95135-5191
LOCALIZAÇÃO: SÃO PAULO

INSTAGRAM: athenas.arq




CONCEITO DO PROJETO:
APRESENTAÇÃO DE PORTFÓLIO

NOME DO PROJETO:
RESIDÊNCIA ATHENAS
TIPO DE PROJETO:
PROJETO ARQUITETÔNICO

DESENHADOR POR:
Natanael Menezes da Silva


APROVADO POR:
Natanael Menezes da Silva

DATA:
01/02/23
ESCALA:
Como indicado
FOLHA:
FL02
FORMATO:
A2

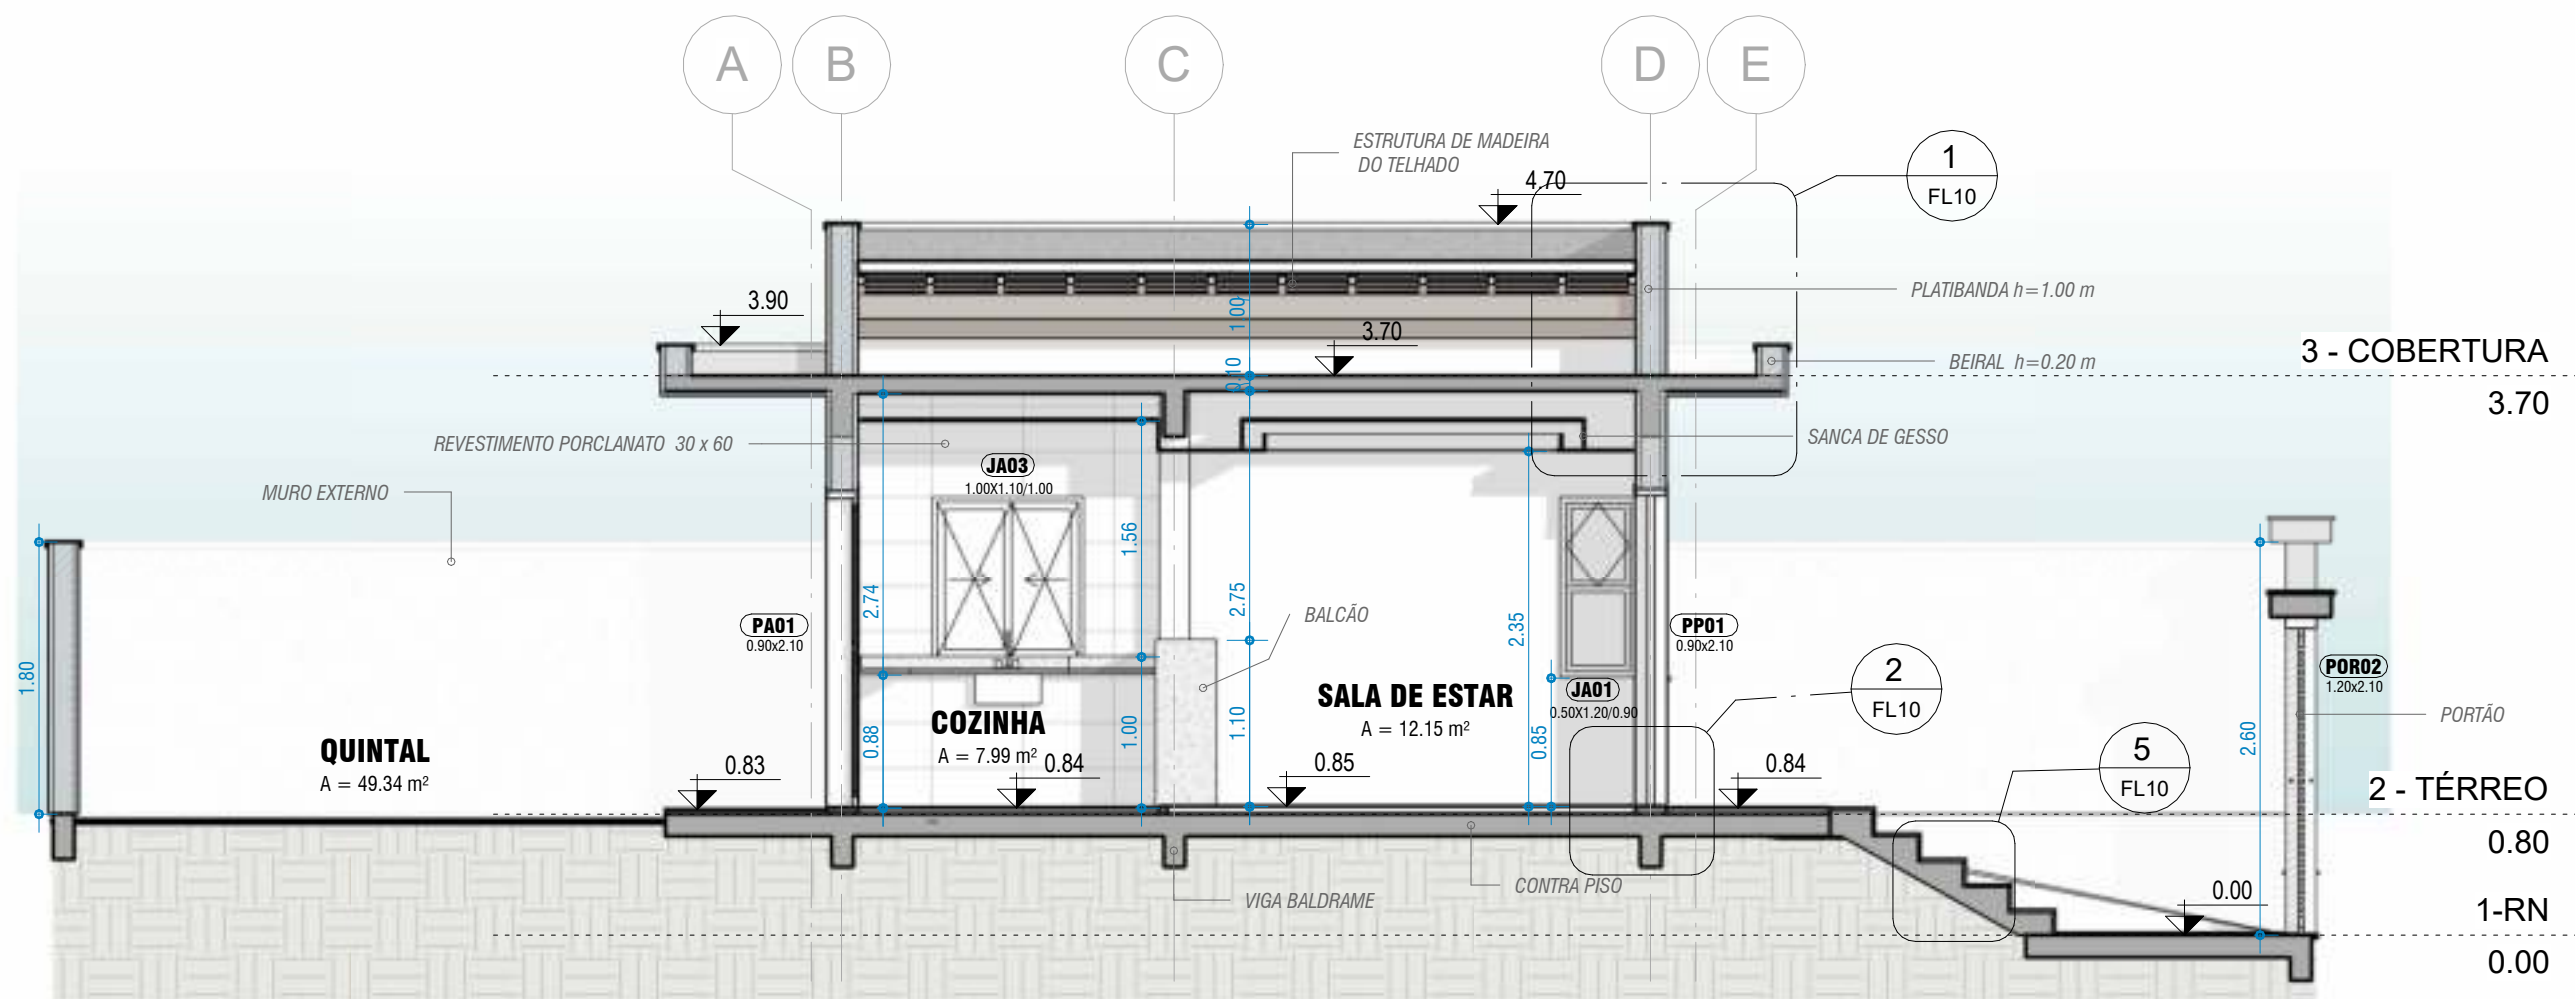

CORTE A-A

ESCALA 1 : 50

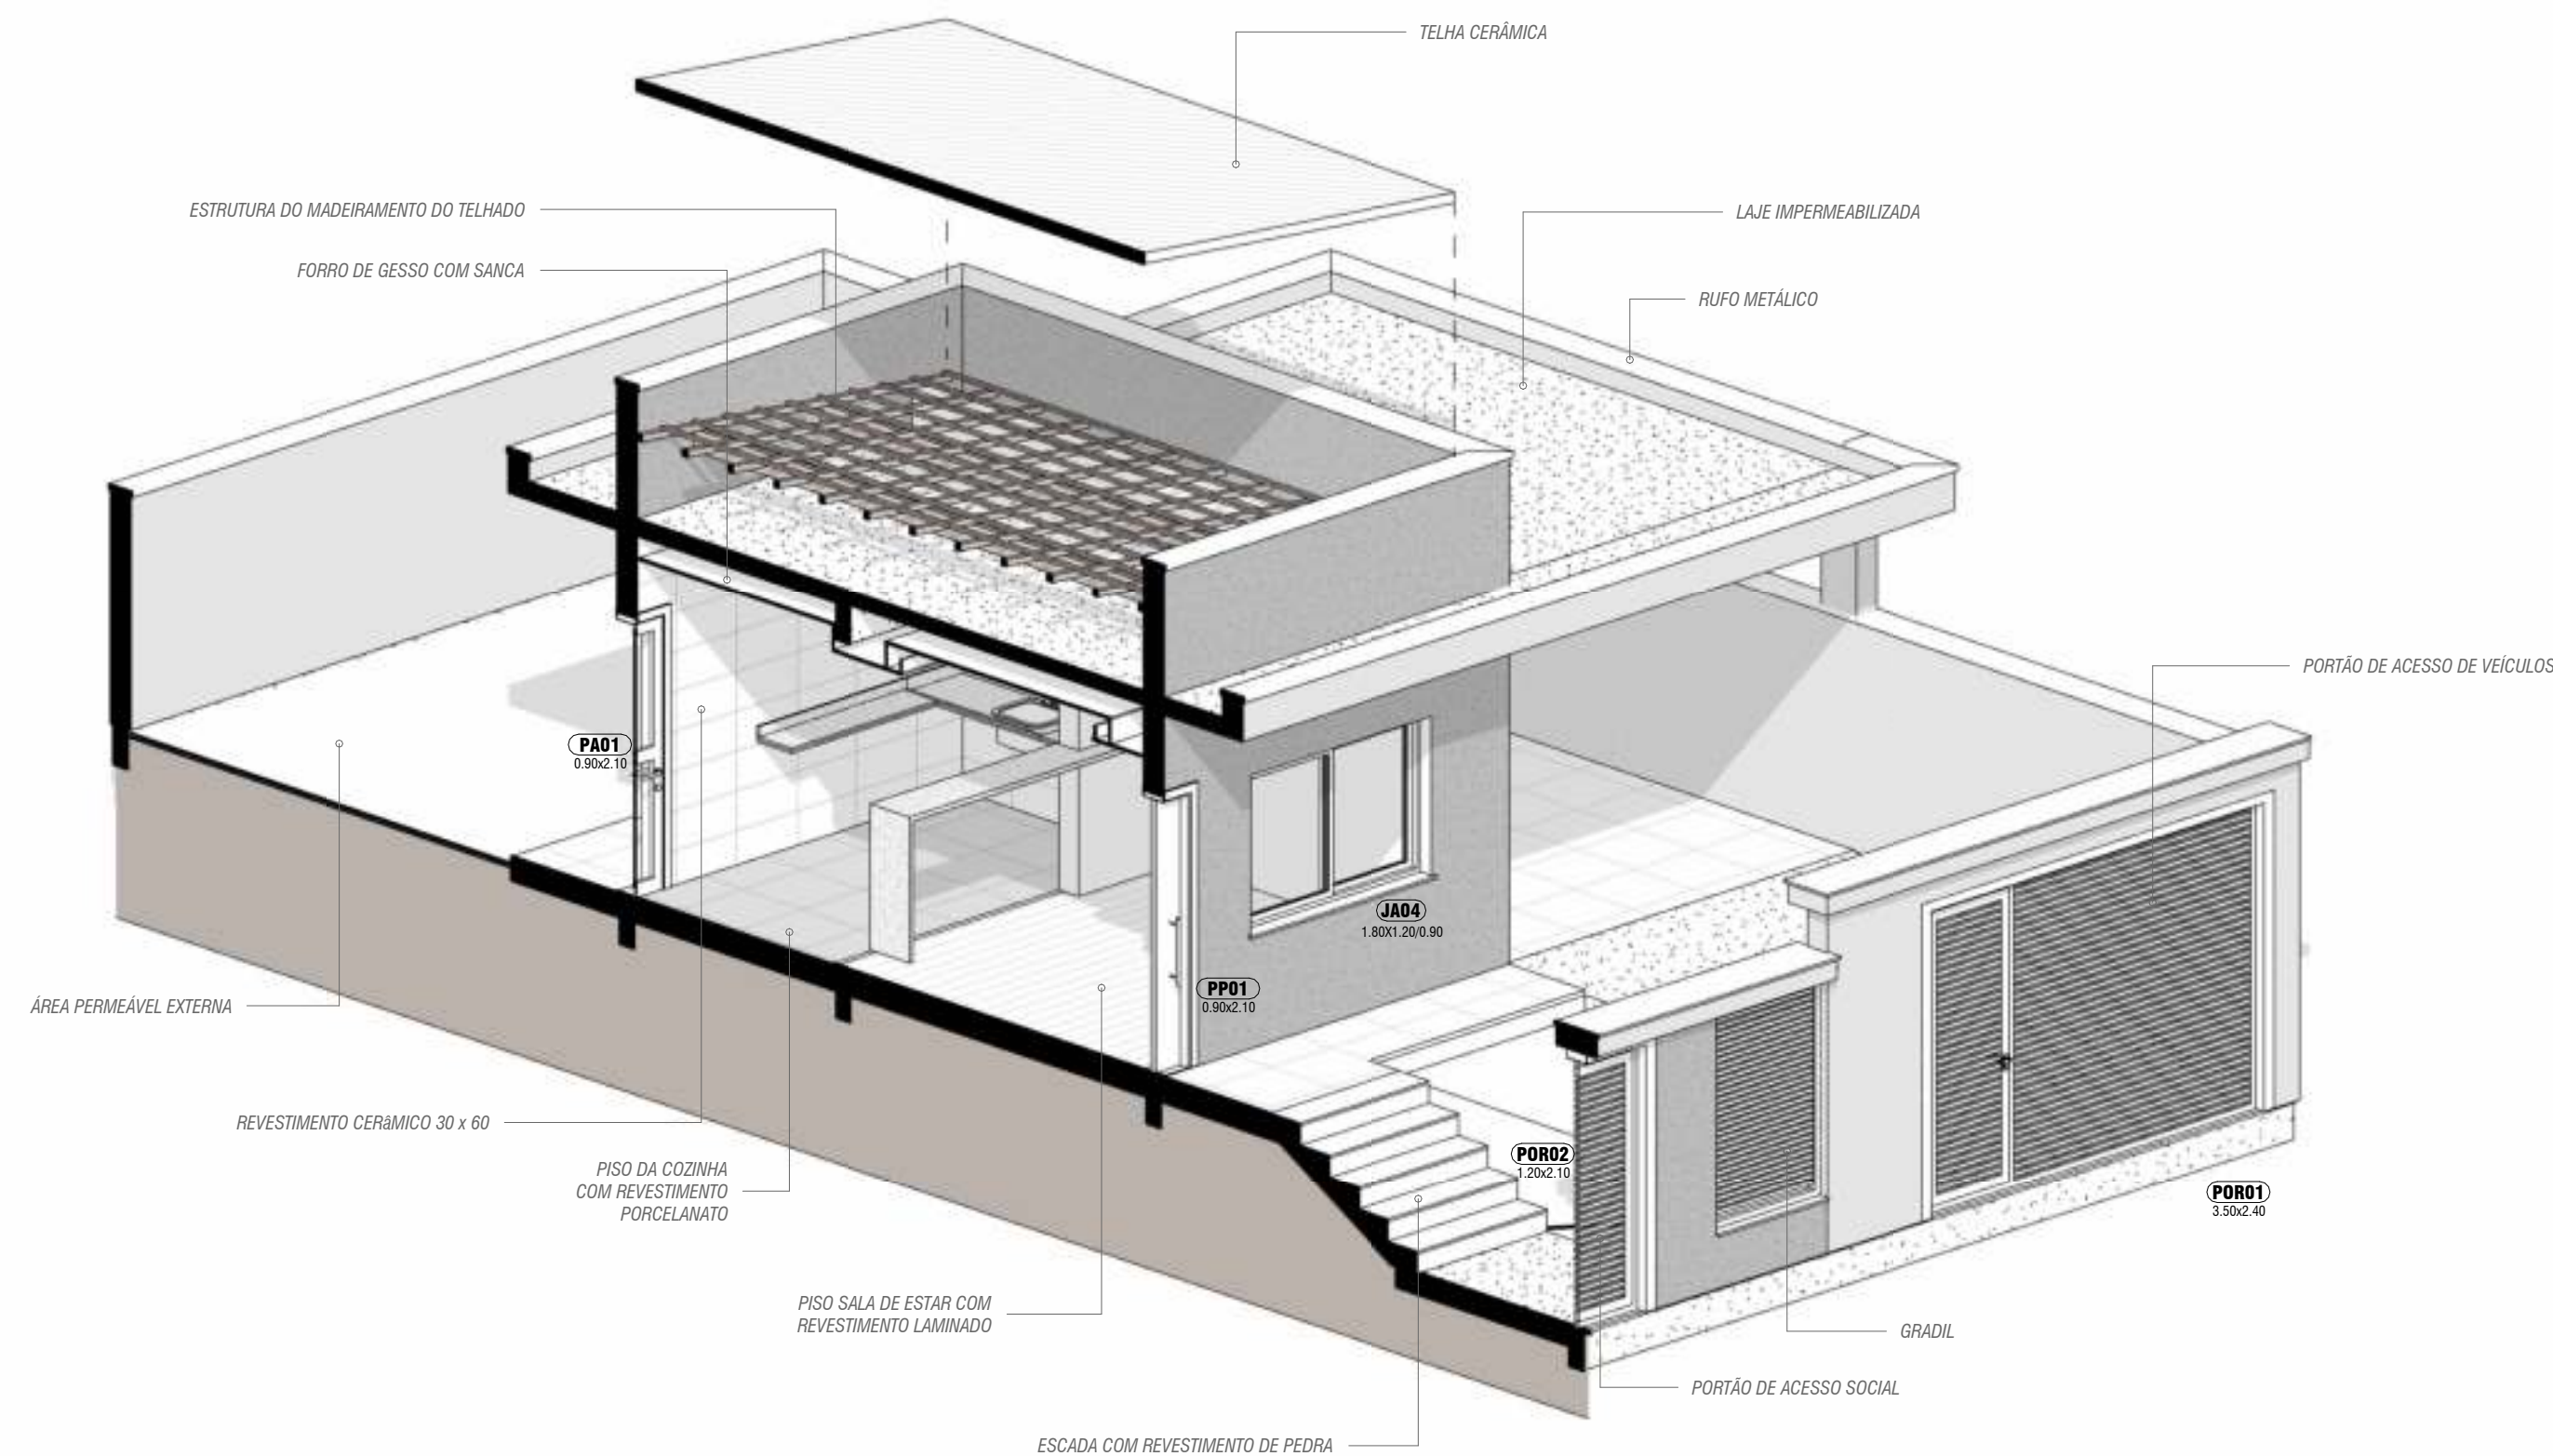

CORTE A-A - ISOMÉTRICO

MATERIAIS DE PAREDES	
MATERIAL	ÁREA
.AZULEJO AREAS MOLHADAS	30.34 m²
.AZULEJO PORCELANATO 30X60	22.47 m²
.BLOCO	217.16 m²
.PINTURA INTERNA	58.67 m²
.PINTURA PROJETADA EXTERNA CLARA	233.41 m²
.PORCELANATO AMADEIRADO EXTERNO	21.14 m²
.TEXTURA PROJETADA EXTERNA COR ESCURA	68.43 m²
ARGAMASSA DE REVESTIMENTO	449.25 m²

MATERIAIS DE PISOS	
MATERIAL	ÁREA
.PEDRA SOLEIRA	6.14 m²
.PINTURA PROJETADA EXTERNA CLARA	5.83 m²
.PISO PORCELANATO MADEIRA	23.14 m²
.PORCELANATO 45X45	3.19 m²
.PORCELANATO 60X60	7.90 m²
.REGULARIZAÇÃO DE CONTRA PISO	66.96 m²
.REVESTIMENTO CERAMICO EXTERNO	32.08 m²

TABELA DE PORTAS				
QT D.	CÓD.	DESCRIÇÃO	LARG.	ALT.
1	PP01	PORTA PIVOTANTE - MADEIRA	0.90	2.10
1	PM03	PORTA DE GIRO - MADEIRA	0.80	2.10
1	PM02	PORTA DE GIRO - MADEIRA	0.70	2.10
1	PA01	PORTA DE GIRO - ALUMÍNIO + VIDRO	0.90	2.10

TABELA DE JANELAS					
QTD.	CÓD.	DESCRIÇÃO	LARG.	ALT.	PEIT ORIL
1	JA01	JANELA BASCULANTE + PEITORIL FIXO - VIDRO	0.50	1.20	0.90
1	JA02	JANELA MAXIM-AR	0.80	0.60	1.50
1	JA03	JANELA 2 FLS CORRER - VIDRO	1.00	1.10	1.00
2	JA04	JANELA 2 FLS CORRER - VIDRO	1.80	1.20	0.90

NATANAEL MENEZES DA SILVA

TELEFONE: (11) 95135-5191
LOCALIZAÇÃO: SÃO PAULO

INSTAGRAM: athenas.arq



CONCEITO DO PROJETO:
APRESENTAÇÃO DE PORTFÓLIO

NOME DO PROJETO:
RESIDÊNCIA ATHENAS
TIPO DE PROJETO:
PROJETO ARQUITETÔNICO

DESENHADOR POR:
Nataanael Menezes da Silva


APROVADO POR:
Nataanael Menezes da Silva

DATA:
01/03/23
ESCALA:
1 : 50

FOLHA:


FL03

FORMATO:
A2

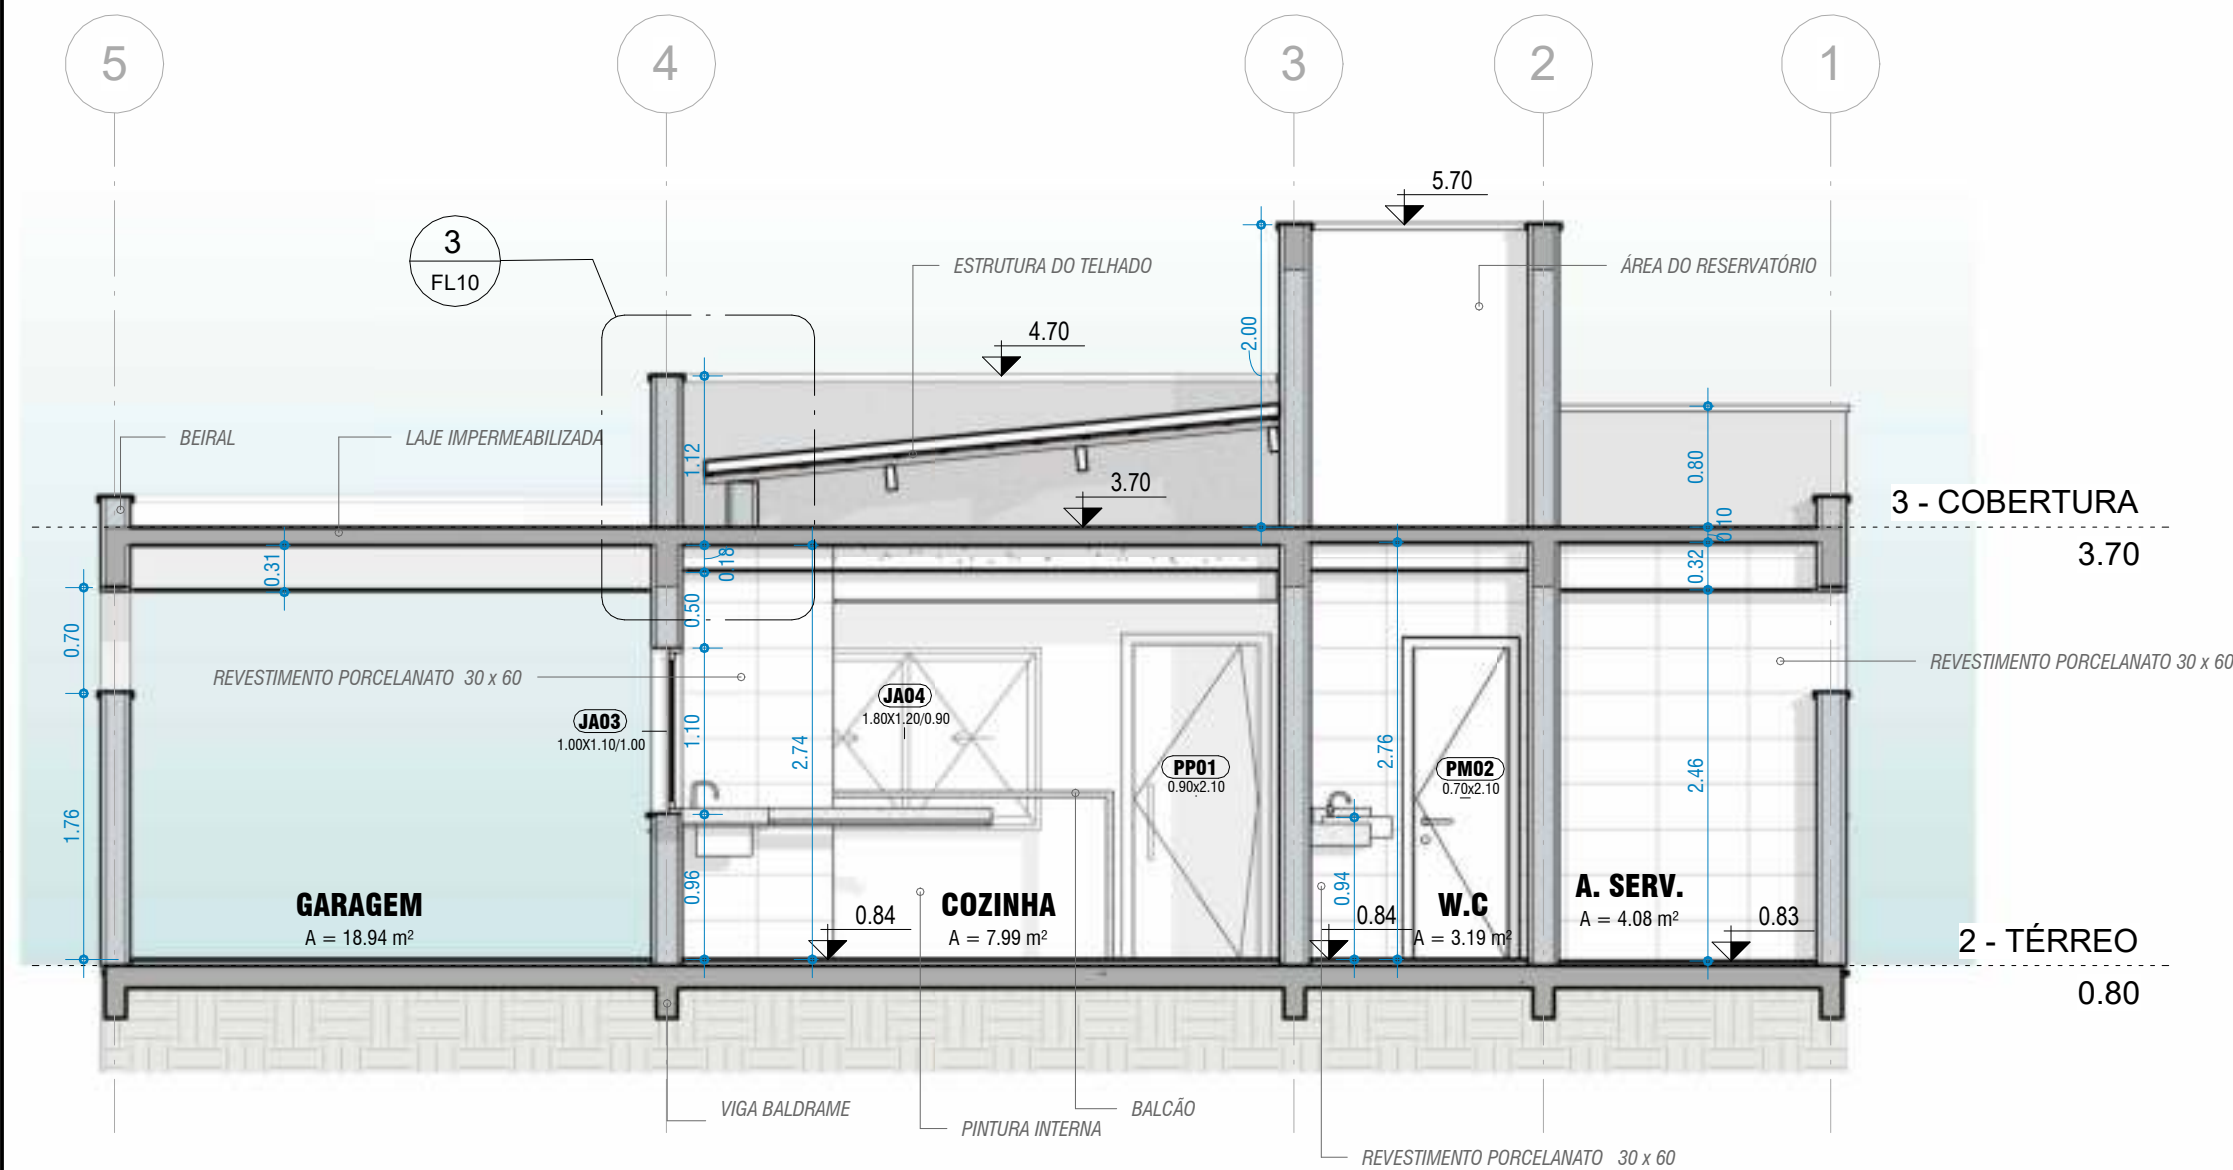

CORTE B-B

ESCALA 1 : 50

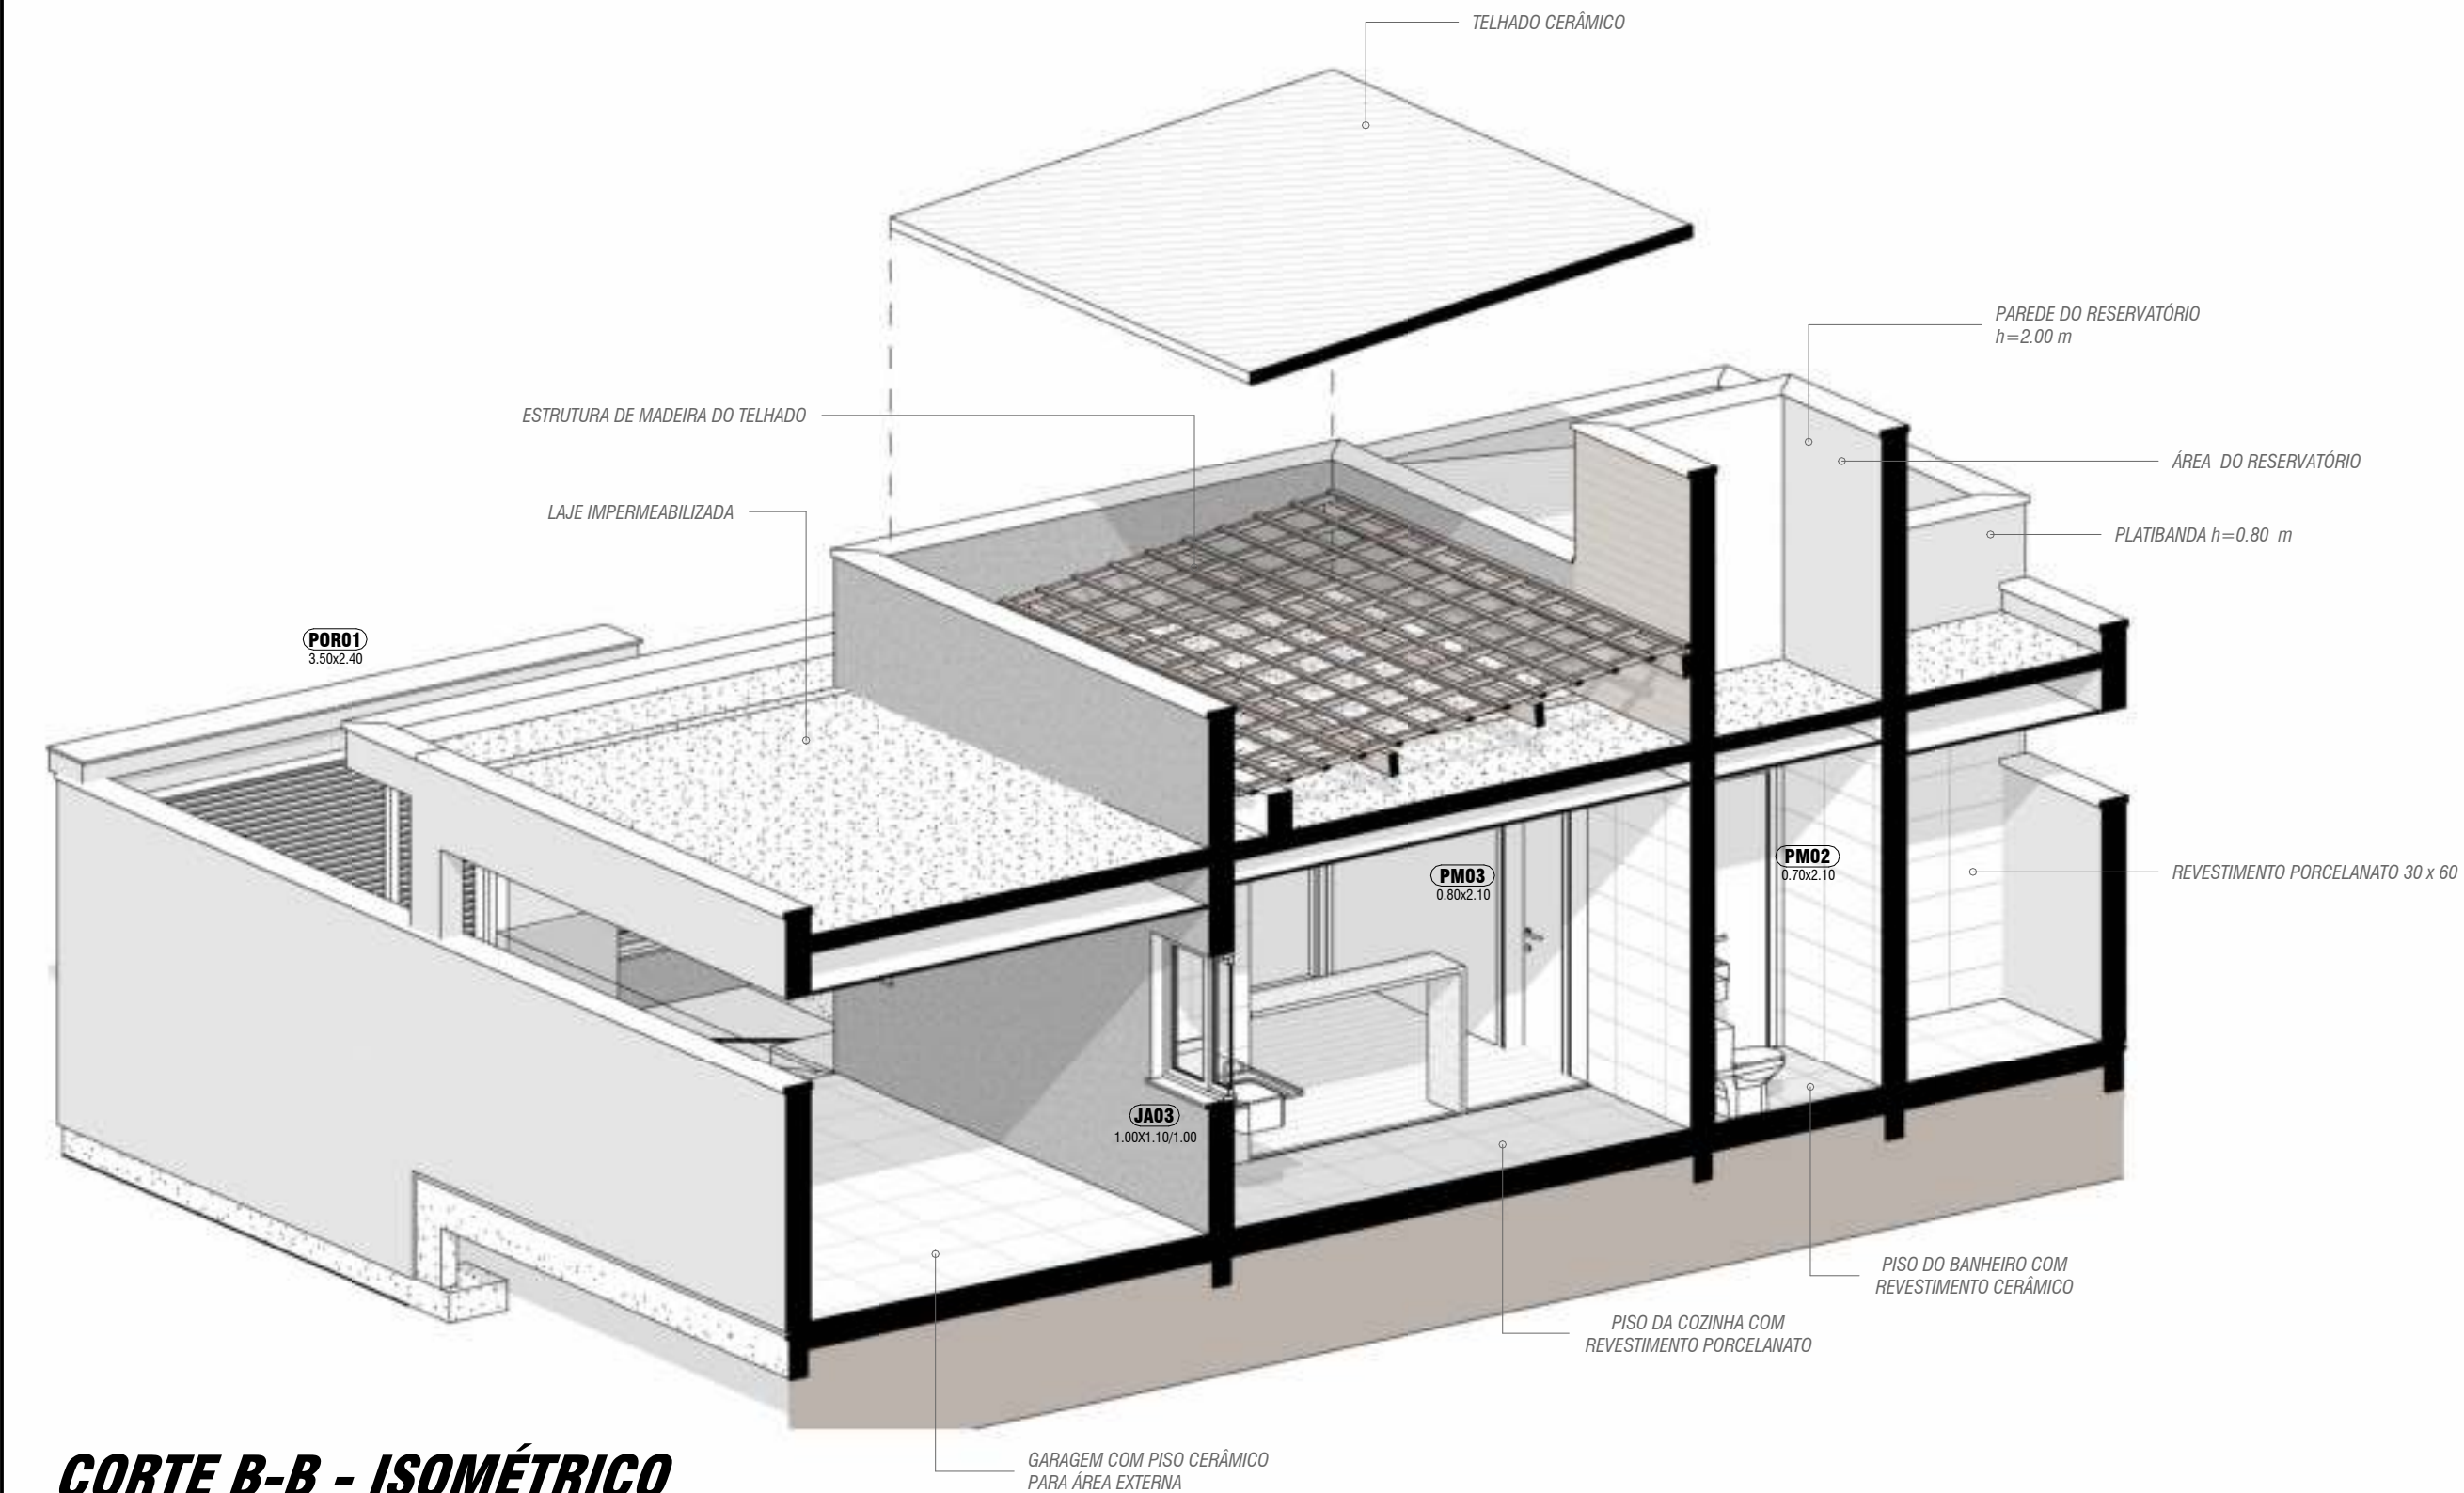

CORTE B-B - ISOMÉTRICO

MATERIAIS DE PAREDES	
MATERIAL	ÁREA
.AZULEJO AREAS MOLHADAS	30.34 m²
.AZULEJO PORCELANATO 30X60	22.47 m²
.BLOCO	217.16 m²
.PINTURA INTERNA	58.67 m²
.PINTURA PROJETADA EXTERNA CLARA	233.41 m²
.PORCELANATO AMADEIRADO EXTERNO	21.14 m²
.TEXTURA PROJETADA EXTERNA COR ESCURA	68.43 m²
ARGAMASSA DE REVESTIMENTO	449.25 m²

MATERIAIS DE PISOS	
MATERIAL	ÁREA
.PEDRA SOLEIRA	6.14 m²
.PINTURA PROJETADA EXTERNA CLARA	5.83 m²
.PISO PORCELANATO MADEIRA	23.14 m²
.PORCELANATO 45X45	3.19 m²
.PORCELANATO 60X60	7.90 m²
.REGULARIZAÇÃO DE CONTRA PISO	66.96 m²
.REVESTIMENTO CERAMICO EXTERNO	32.08 m²

TABELA DE JANELAS					
QTD.	CÓD.	DESCRIÇÃO	LARG.	ALT.	PEIT ORIL
1	JA01	JANELA BASCULANTE + PEITORIL FIXO - VIDRO	0.50	1.20	0.90
1	JA02	JANELA MAXIM-AR	0.80	0.60	1.50
1	JA03	JANELA 2 FLS CORRER - VIDRO	1.00	1.10	1.00
2	JA04	JANELA 2 FLS CORRER - VIDRO	1.80	1.20	0.90

TABELA DE PORTAS				
QT D.	CÓD.	DESCRIÇÃO	LARG.	ALT.
1	PP01	PORTA PIVOTANTE - MADEIRA	0.90	2.10
1	PM03	PORTA DE GIRO - MADEIRA	0.80	2.10
1	PM02	PORTA DE GIRO - MADEIRA	0.70	2.10
1	PA01	PORTA DE GIRO - ALUMÍNIO + VIDRO	0.90	2.10

NATANAEL MENEZES DA SILVA

TELEFONE: (11) 95135-5191
LOCALIZAÇÃO: SÃO PAULO

INSTAGRAM: athenas.arq



CONCEITO DO PROJETO:
APRESENTAÇÃO DE PORTFÓLIO

NOME DO PROJETO:
RESIDÊNCIA ATHENAS
TIPO DE PROJETO:
PROJETO ARQUITETÔNICO

DESENHADOR POR:
Natanael Menezes da Silva


APROVADO POR:
Natanael Menezes da Silva

DATA:
01/03/23
ESCALA:
1 : 50


FOLHA:

FL04

FORMATO:
A2

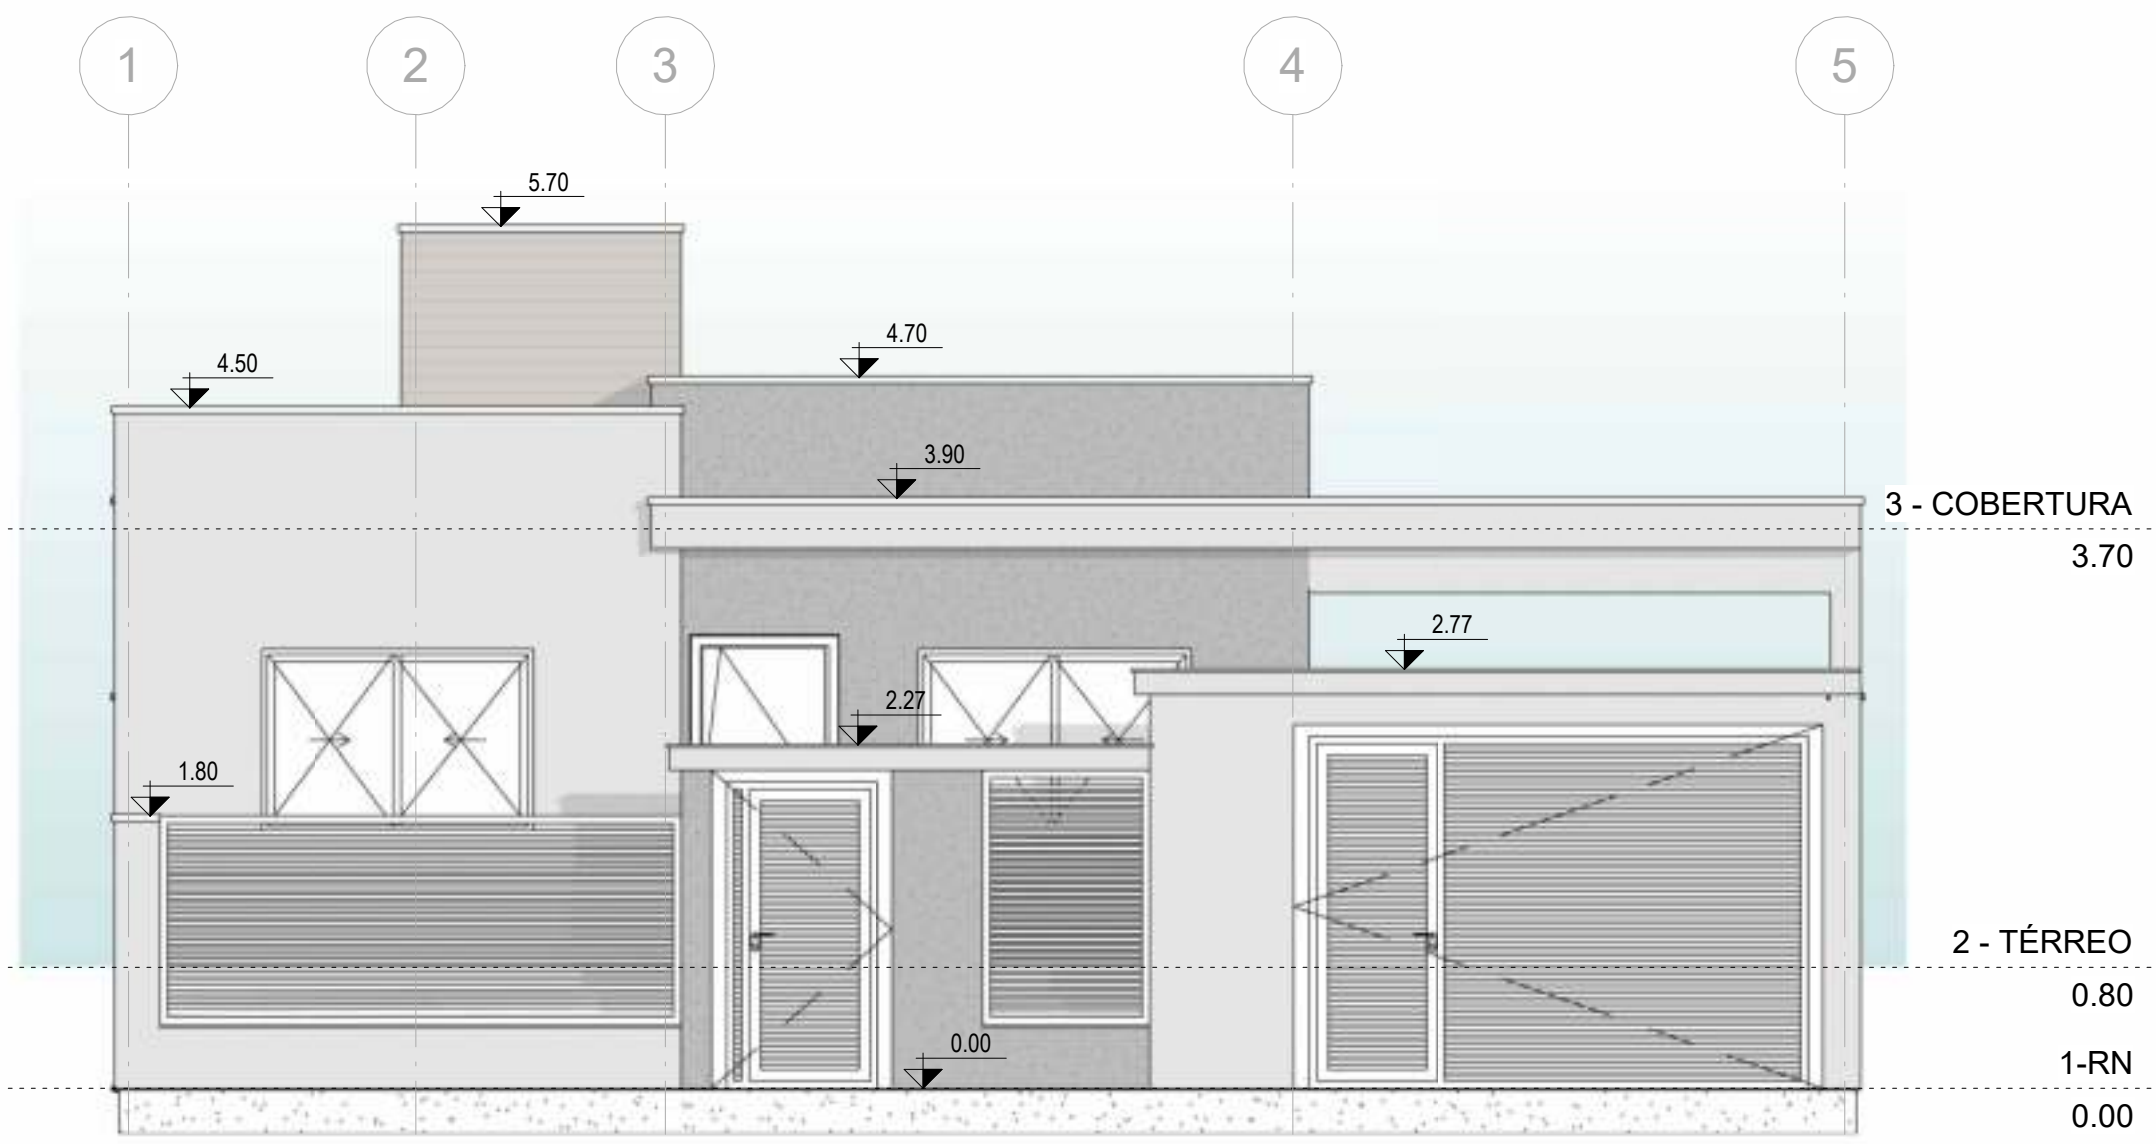

RENDERIZAÇÃO FACHADA 01

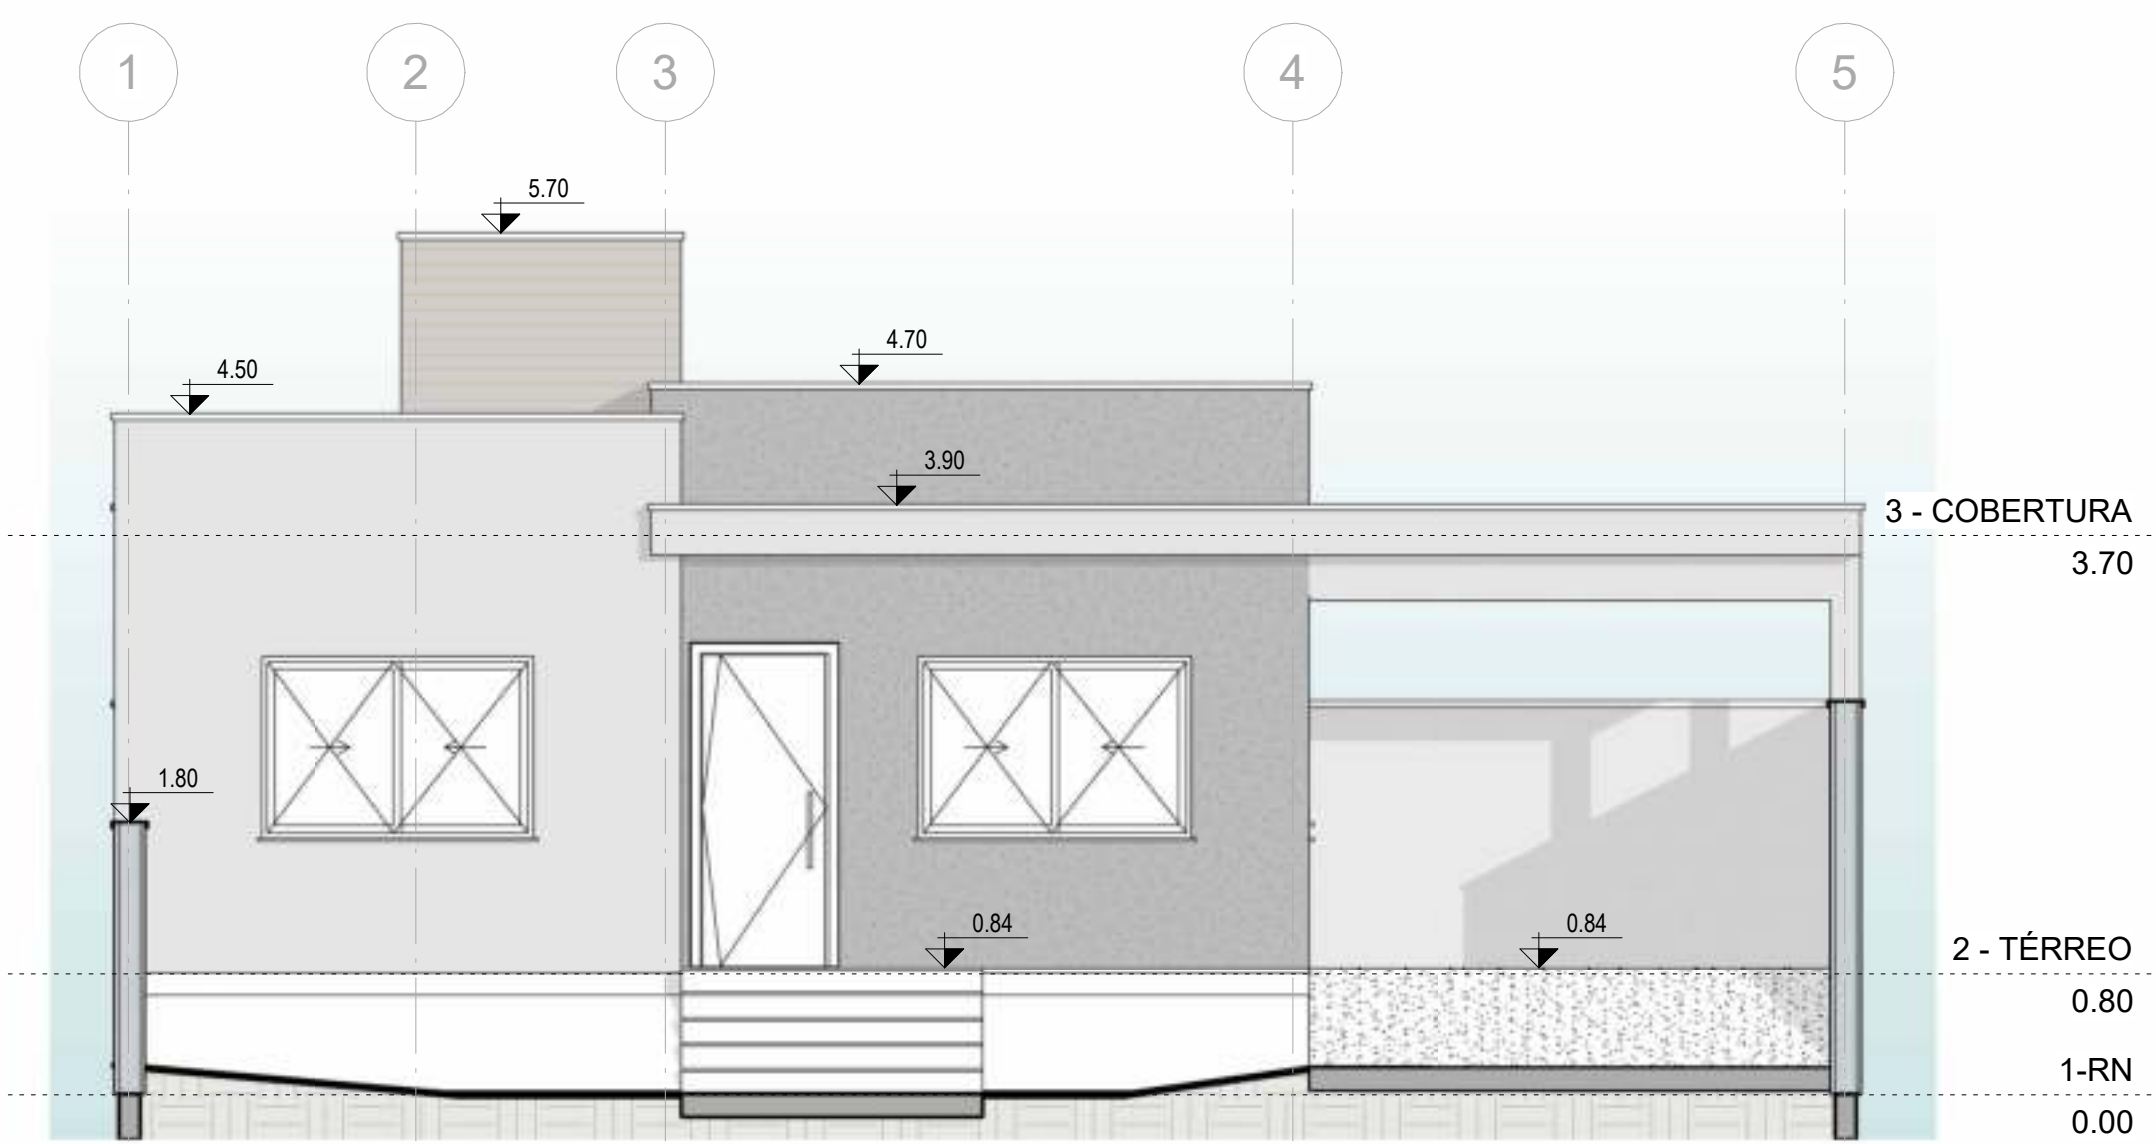

RENDERIZAÇÃO FACHADA 02

NATANAEL MENEZES DA SILVA

TELEFONE: (11) 95135-5191
LOCALIZAÇÃO: SÃO PAULO

INSTAGRAM: athenas.arq



CONCEITO DO PROJETO:
APRESENTAÇÃO DE PORTFÓLIO

NOME DO PROJETO:
RESIDÊNCIA ATHENAS
TIPO DE PROJETO:
PROJETO ARQUITETÔNICO

DESENHADOR POR:
Natanael Menezes da Silva


APROVADO POR:
Natanael Menezes da Silva

DATA:
01/04/23
ESCALA:
Como indicado

FOLHA:

FL06

FORMATO:
A2

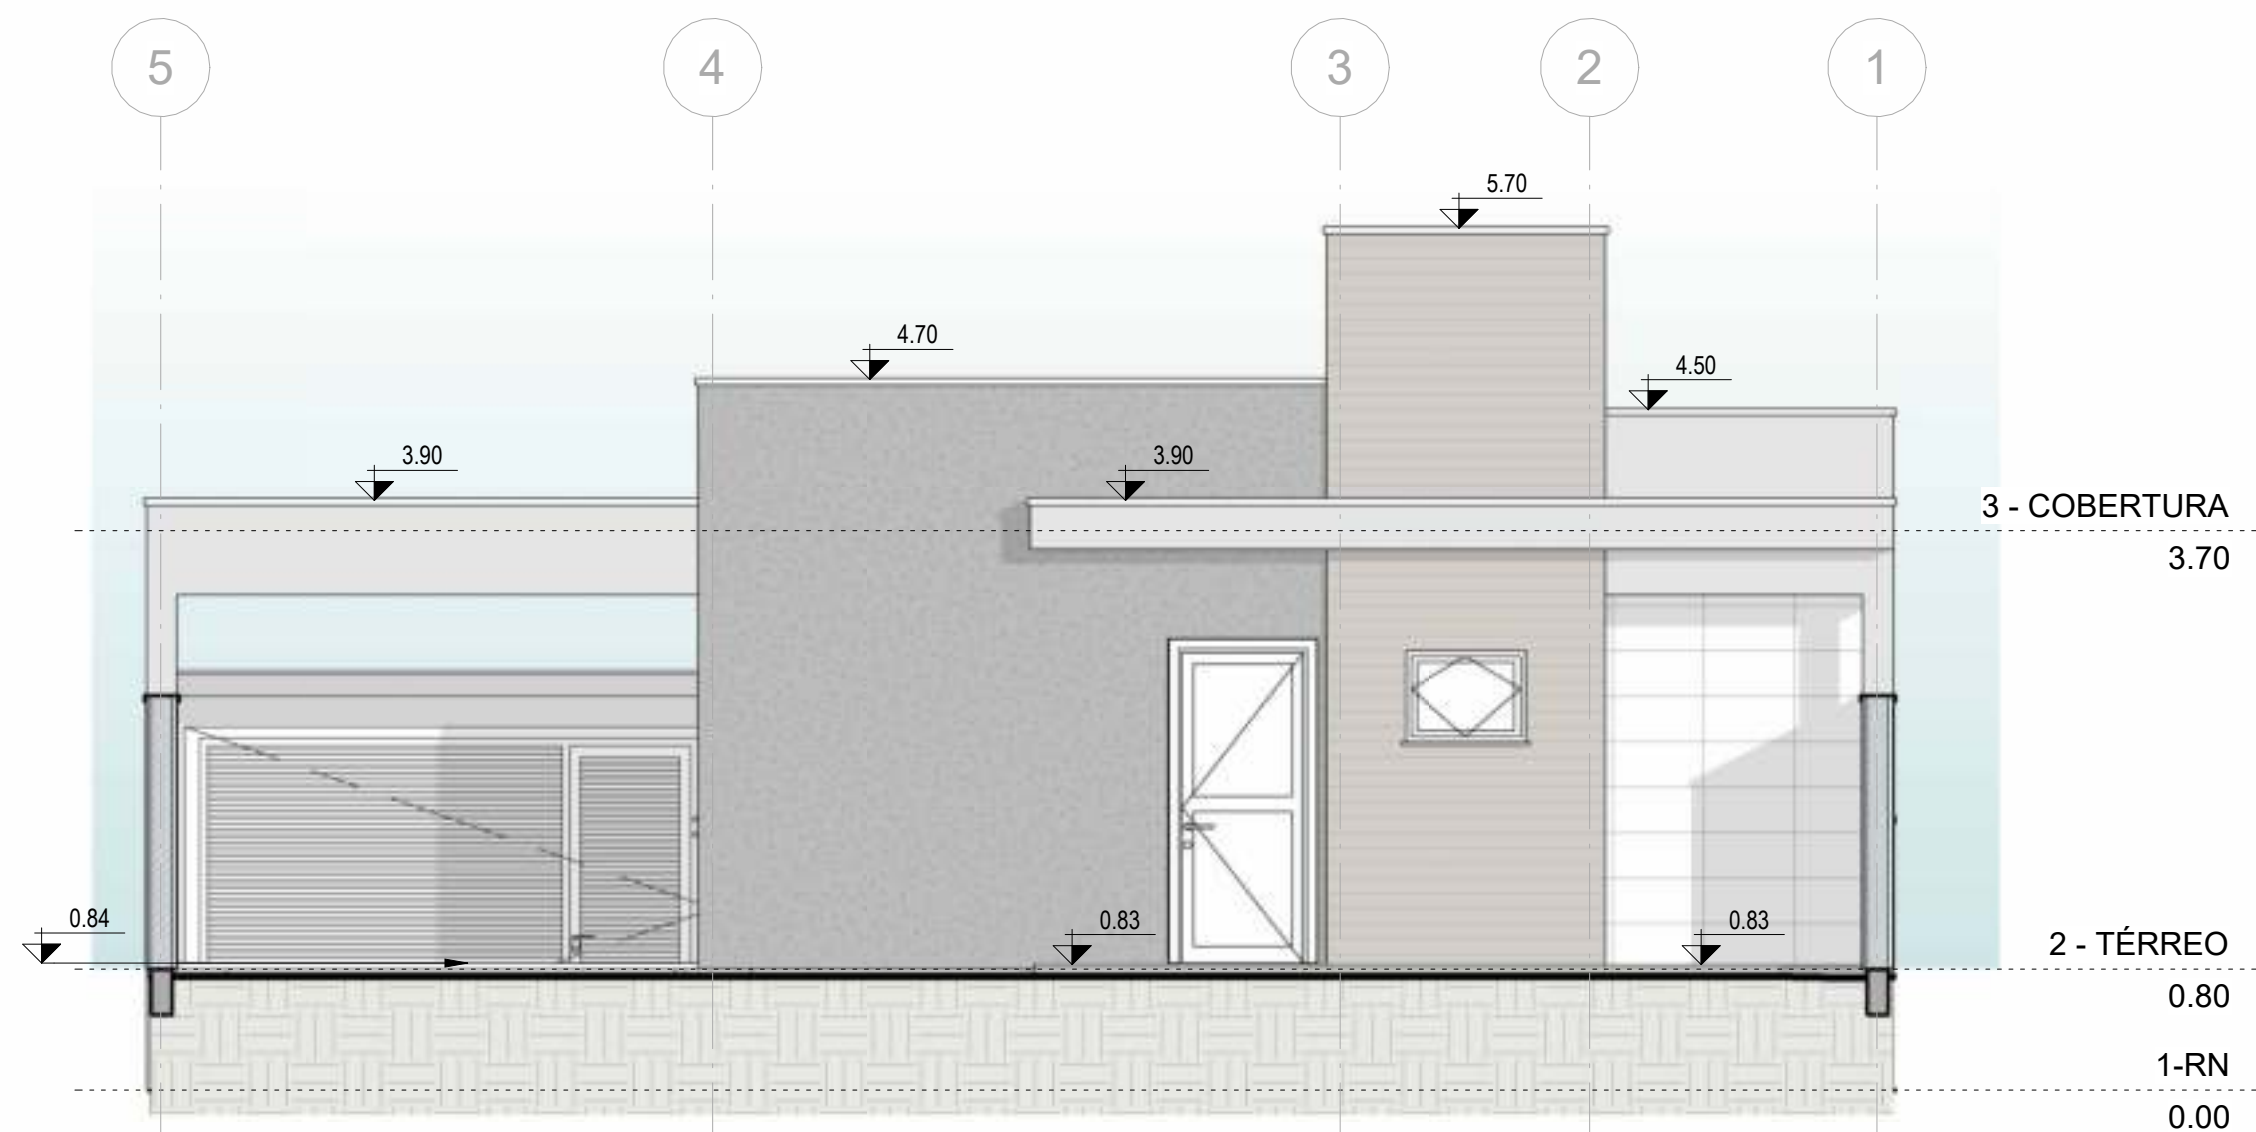

FACHADA POSTERIOR

ESCALA 1:50



PERSPECTIVA FACHADA POSTERIOR

NATANAEL MENEZES DA SILVA

TELEFONE: (11) 95135-5191
LOCALIZAÇÃO: SÃO PAULO

INSTAGRAM: athenas.arq



CONCEITO DO PROJETO:
APRESENTAÇÃO DE PORTFÓLIO

NOME DO PROJETO:
RESIDÊNCIA ATHENAS
TIPO DE PROJETO:
PROJETO ARQUITETÔNICO

DESENHADOR POR:
Natanael Menezes da Silva

APROVADO POR:
Natanael Menezes da Silva

DATA:
01/04/23

ESCALA:
Como indicado

FOLHA:

FL07

FORMATO:
A2



1 : 50




ESCALA 1 : 50



8	CAIBROS 5x5cm	3.22
12	CAIBROS 5x5cm	3.82
11	RIPAS 2x5cm	3.25
13	RIPAS 2x5cm	5.15
3	TERÇAS 6x16cm	3.25
3	TERÇAS 6x16cm	5.15


FL08

FORMATO: **A2**

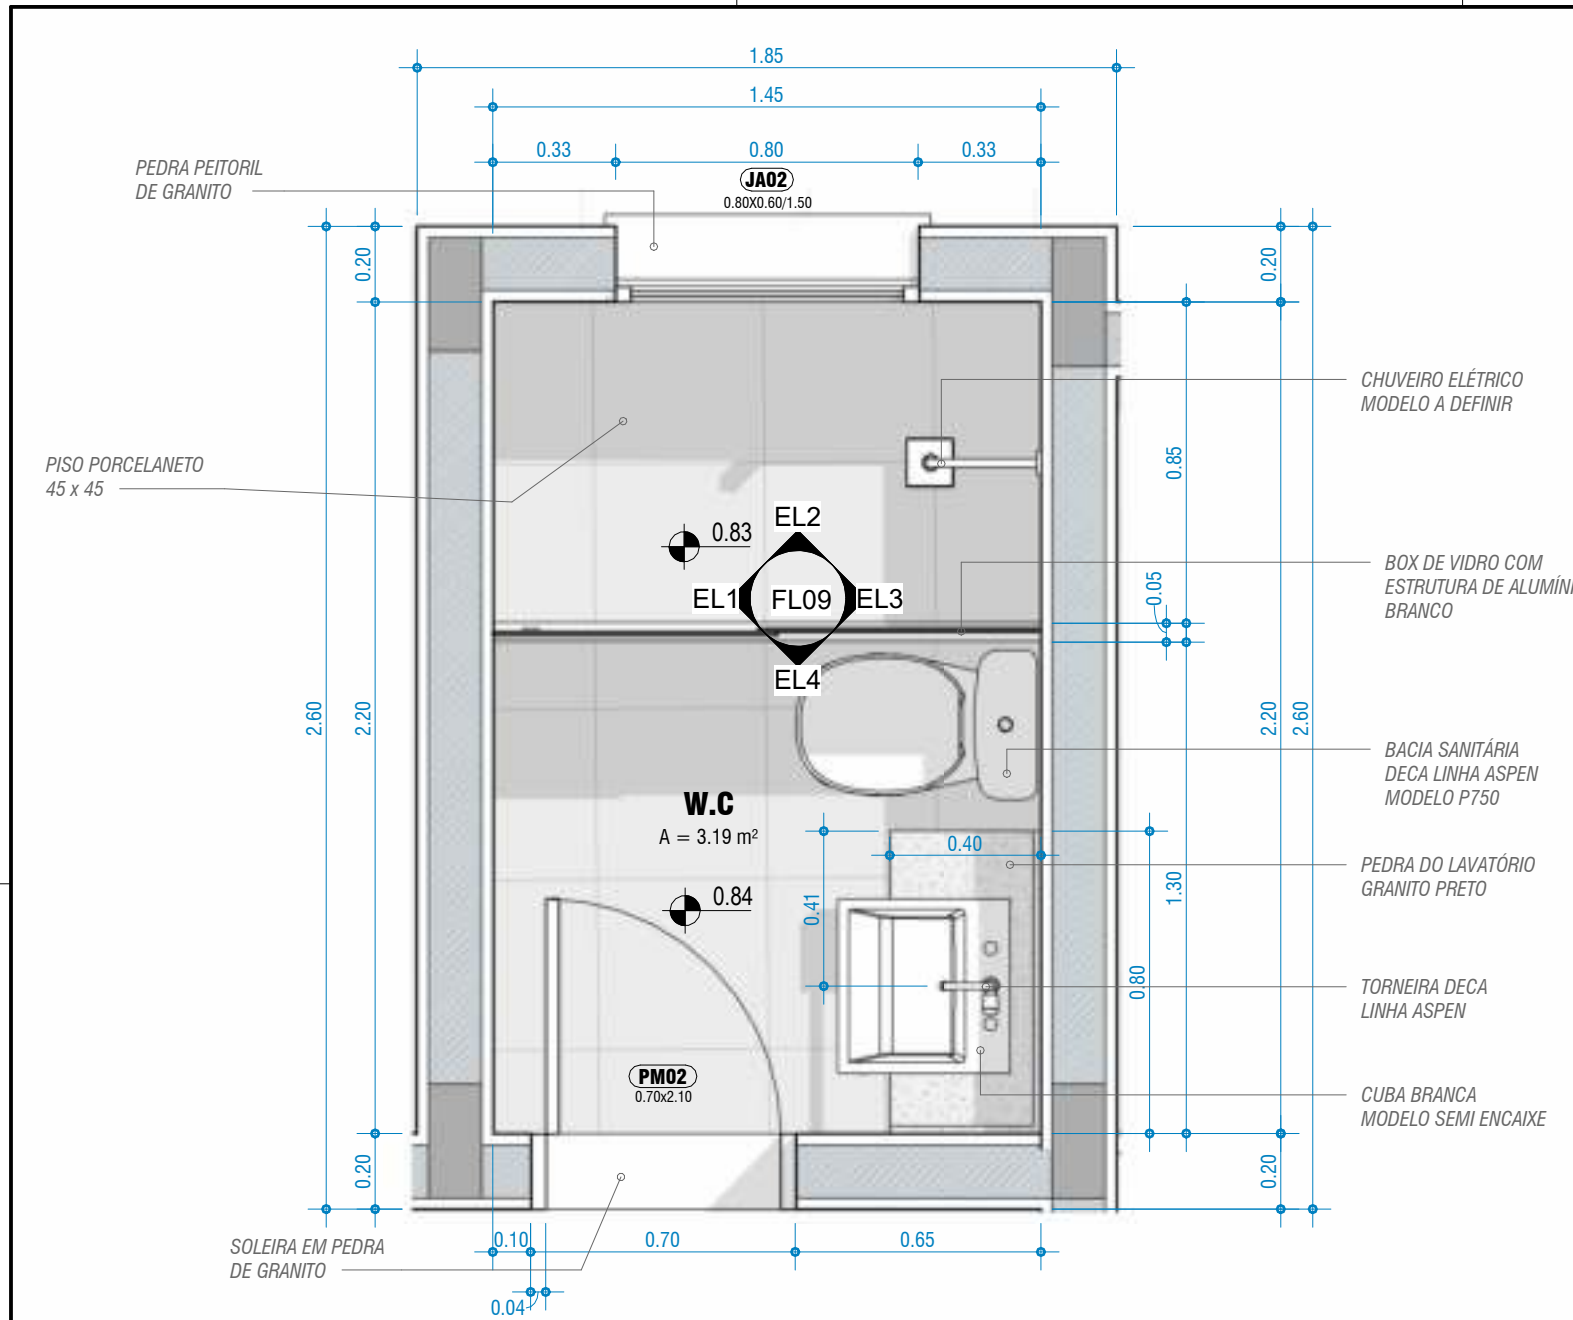


DET. B - PLANTA DETALHE W.C

1 : 20

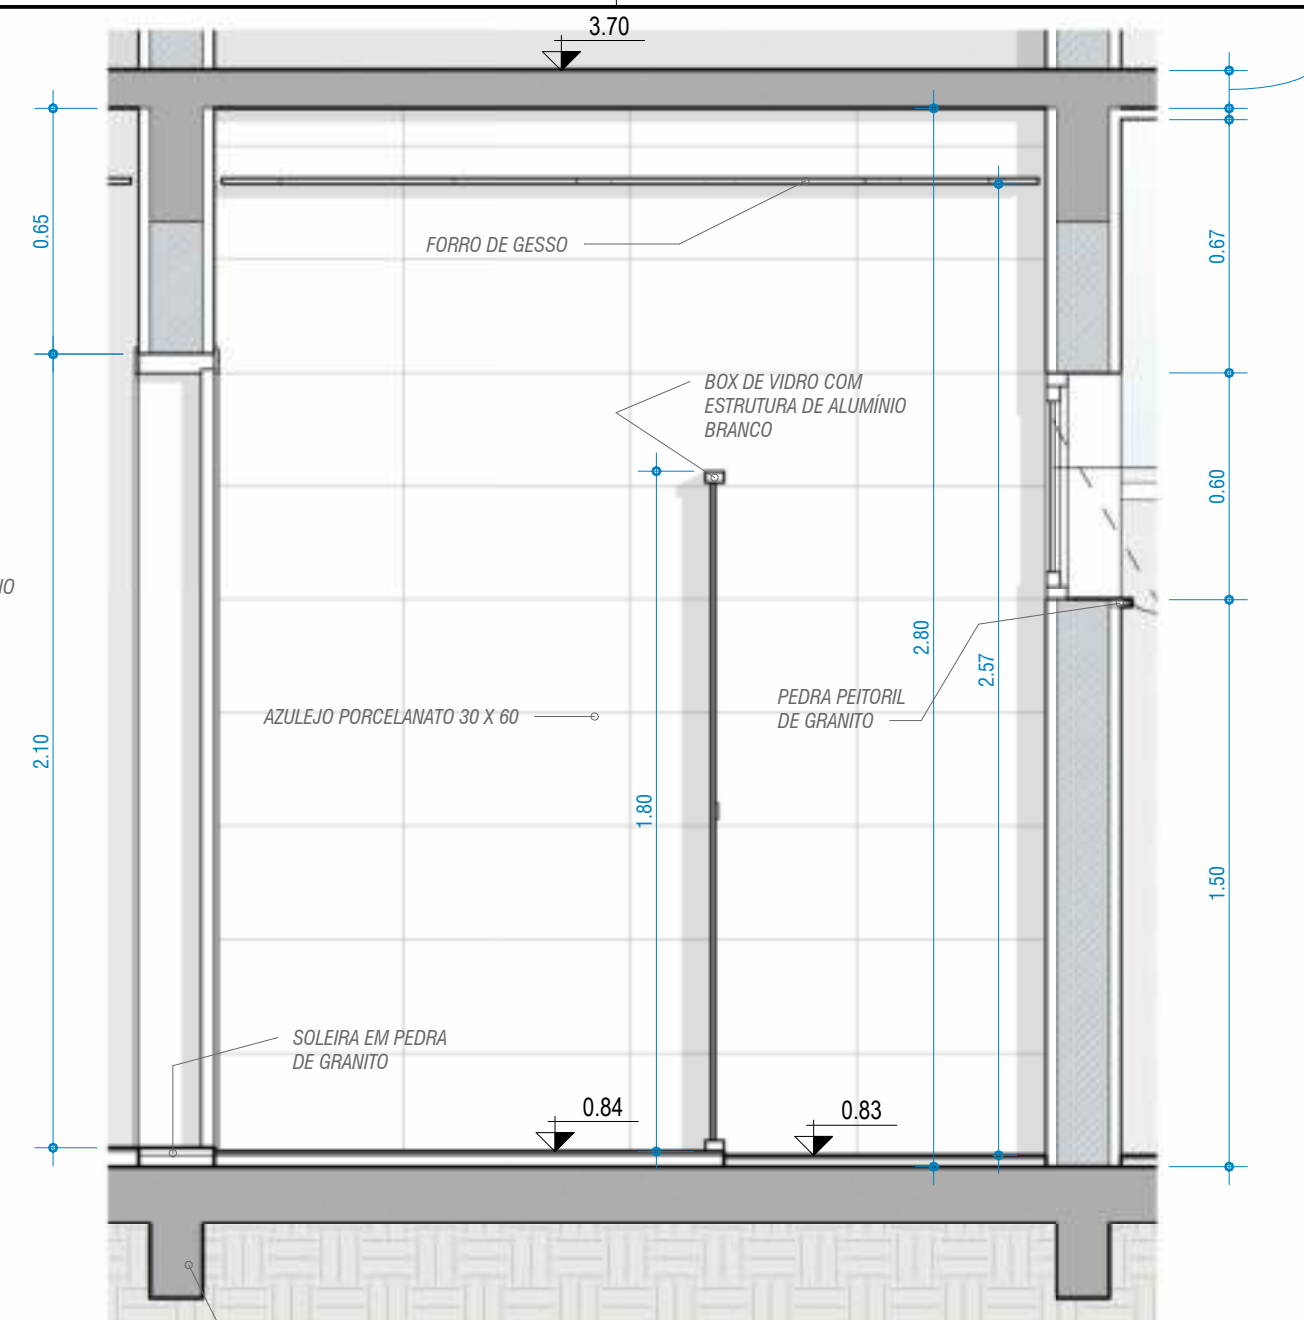


EL. 01

ESCALA 1 : 20

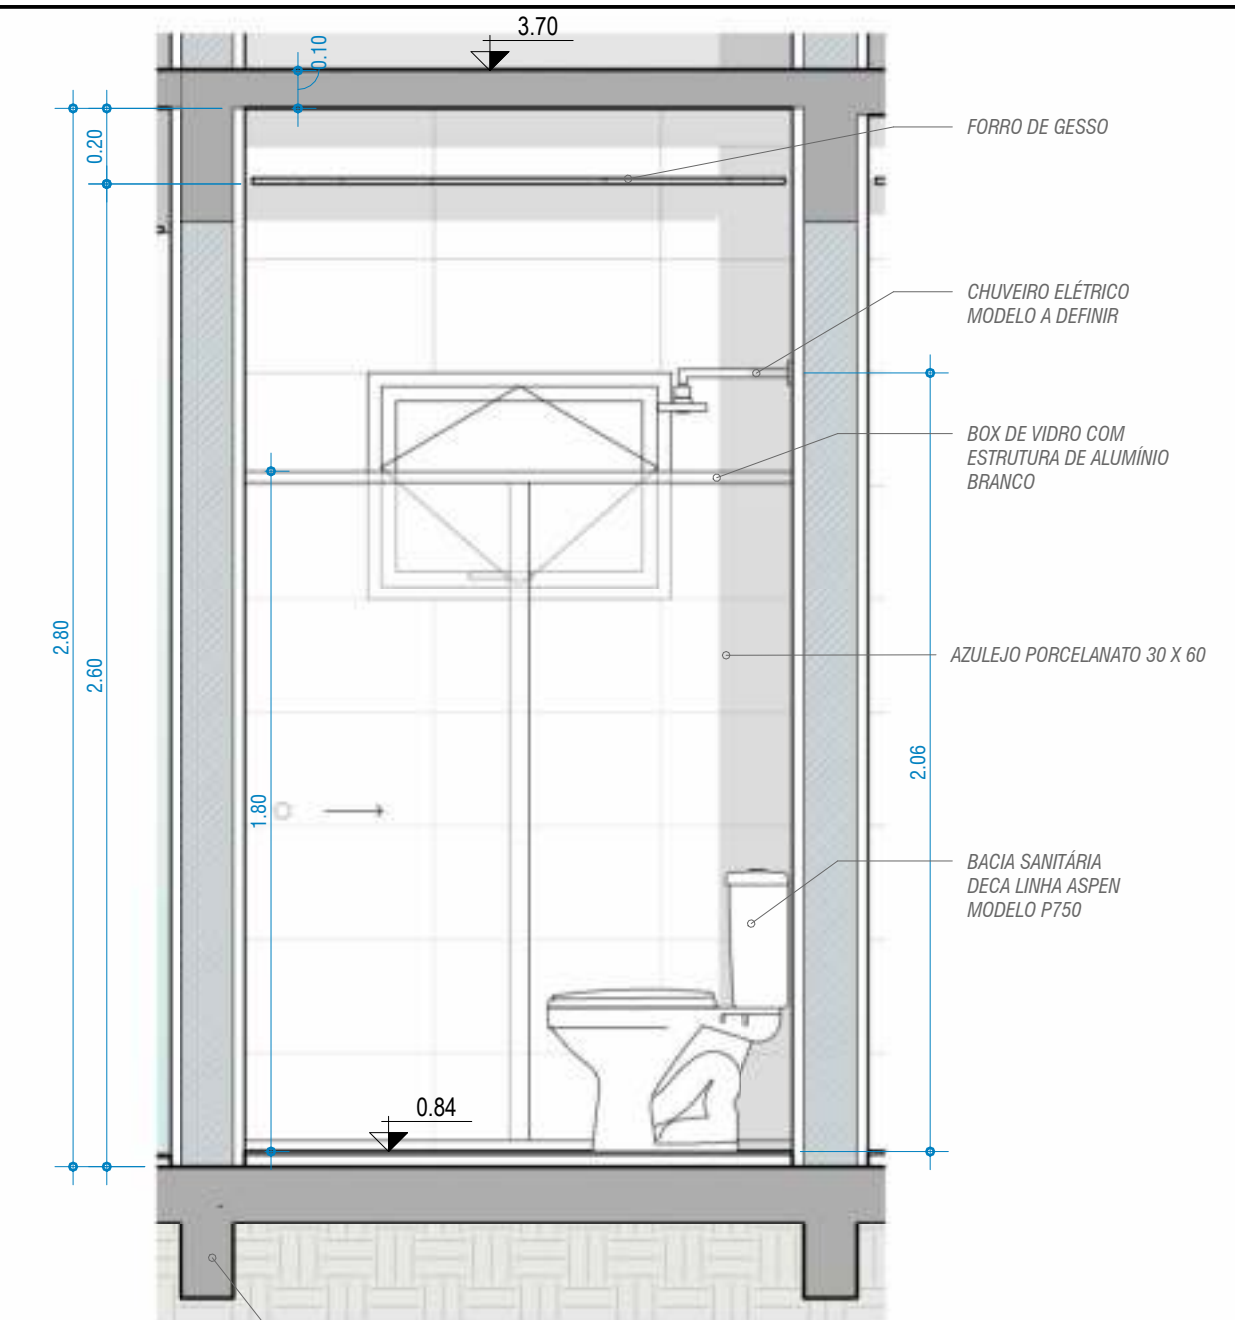


EL. 02

ESCALA 1 : 20

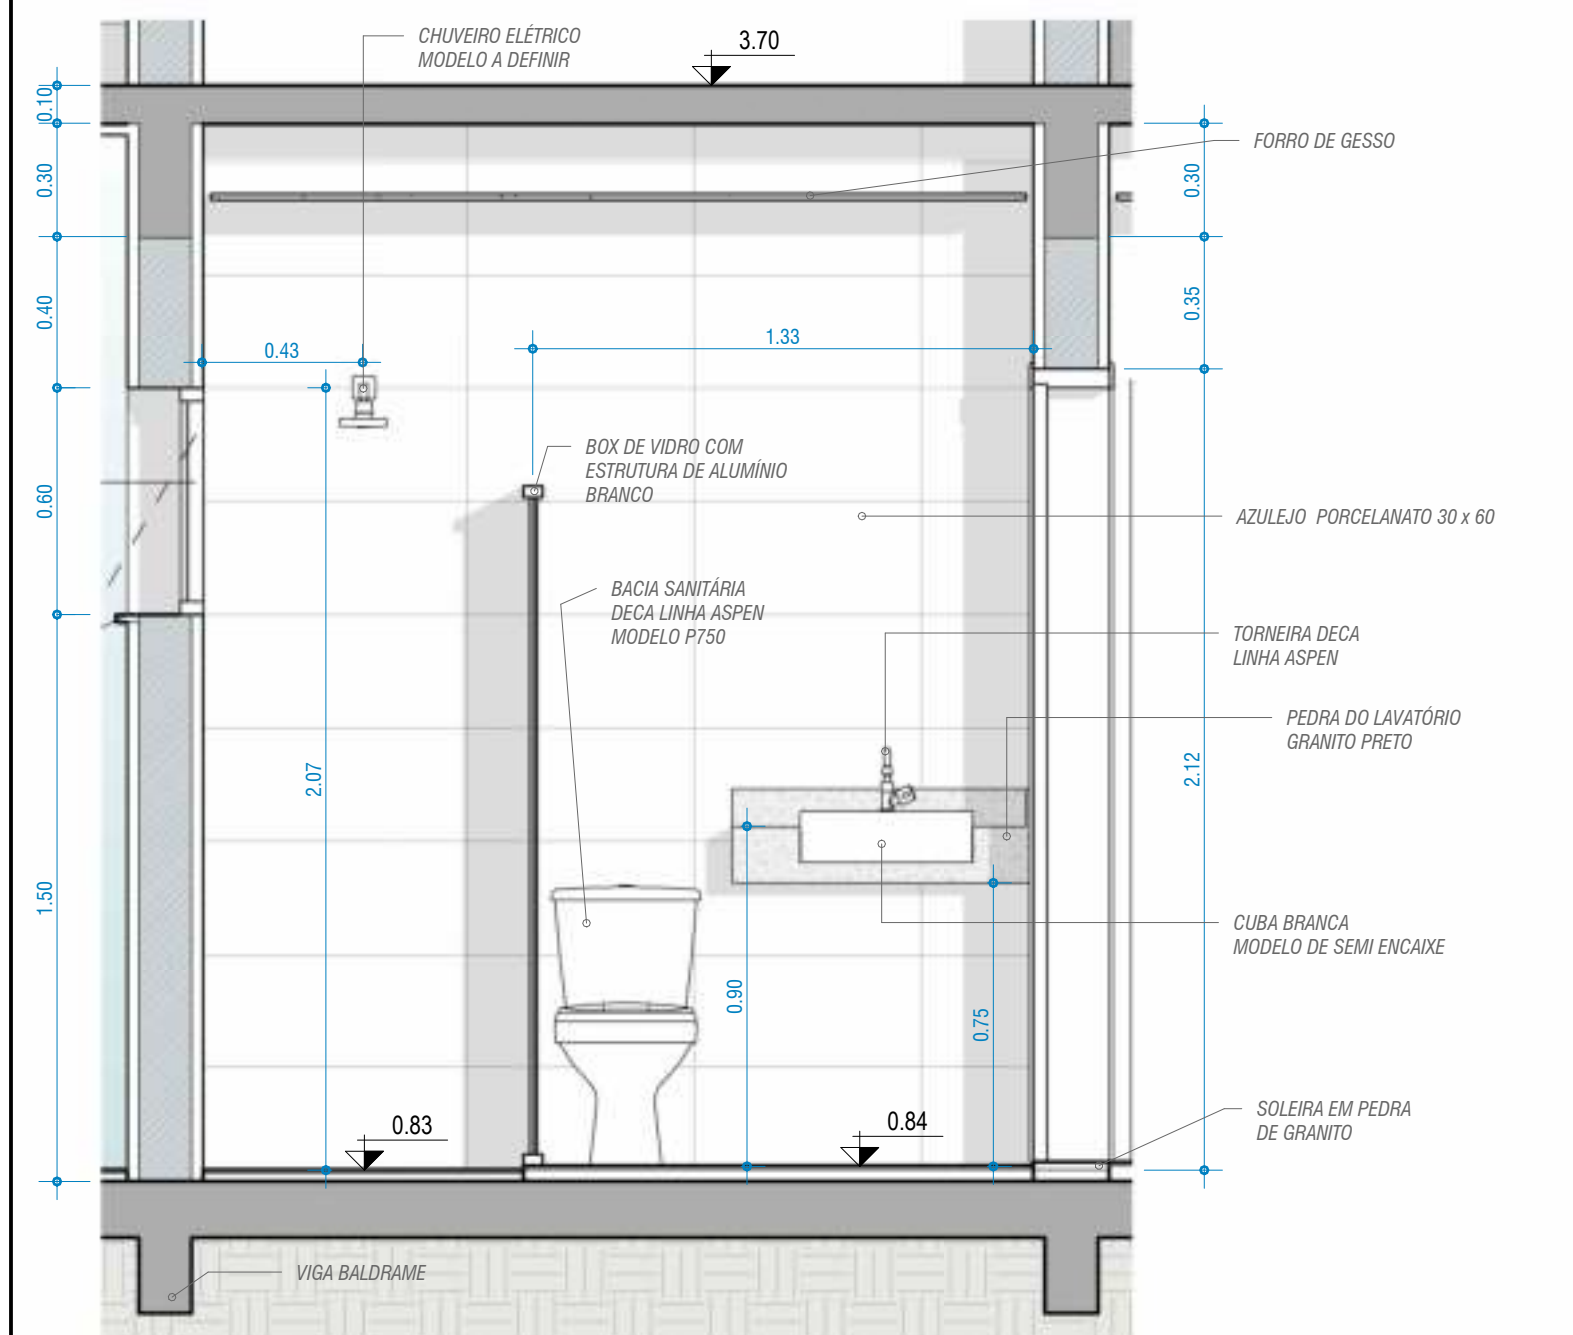


EL. 03

ESCALA 1 : 20

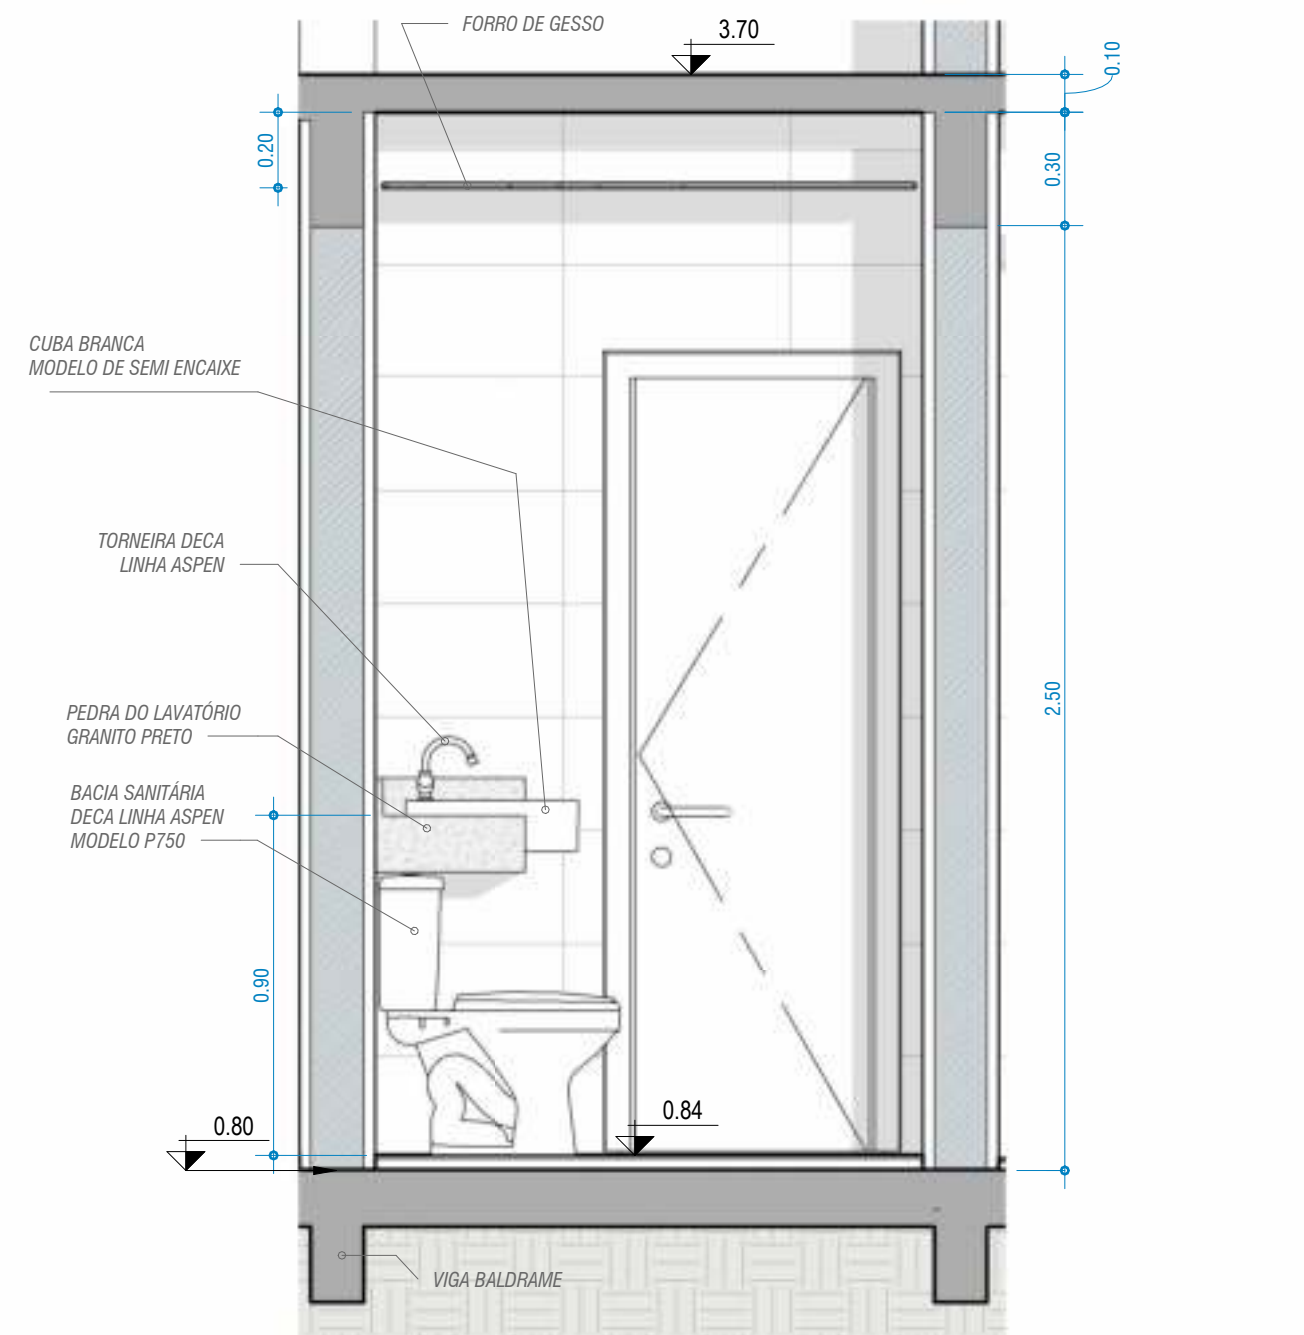

EL. 04

ESCALA 1 : 20

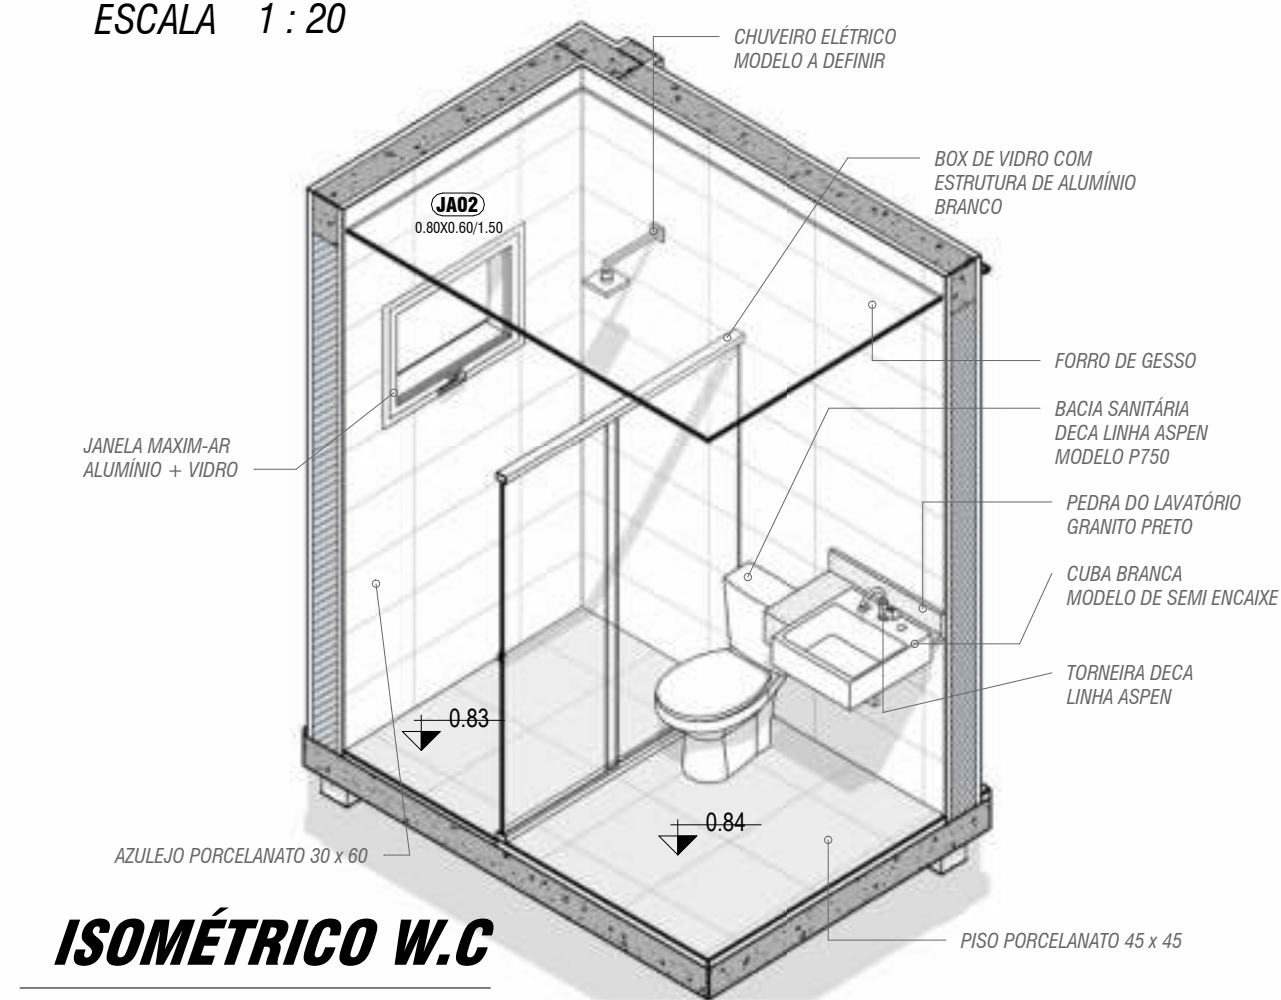

ISOMÉTRICO W.C

NATANAEL MENEZES DA SILVA

TELEFONE: (11) 95135-5191
LOCALIZAÇÃO: SÃO PAULO

INSTAGRAM: athenas.arq



CONCEITO DO PROJETO:
APRESENTAÇÃO DE PORTFÓLIO

NOME DO PROJETO:
RESIDÊNCIA ATHENAS
TIPO DE PROJETO:
PROJETO ARQUITETÔNICO

DESENHADOR POR:
Natanael Menezes da Silva


APROVADO POR:
Natanael Menezes da Silva

DATA:
01/05/23
ESCALA:
1 : 20

FOLHA:


FL09

FORMATO:
A2

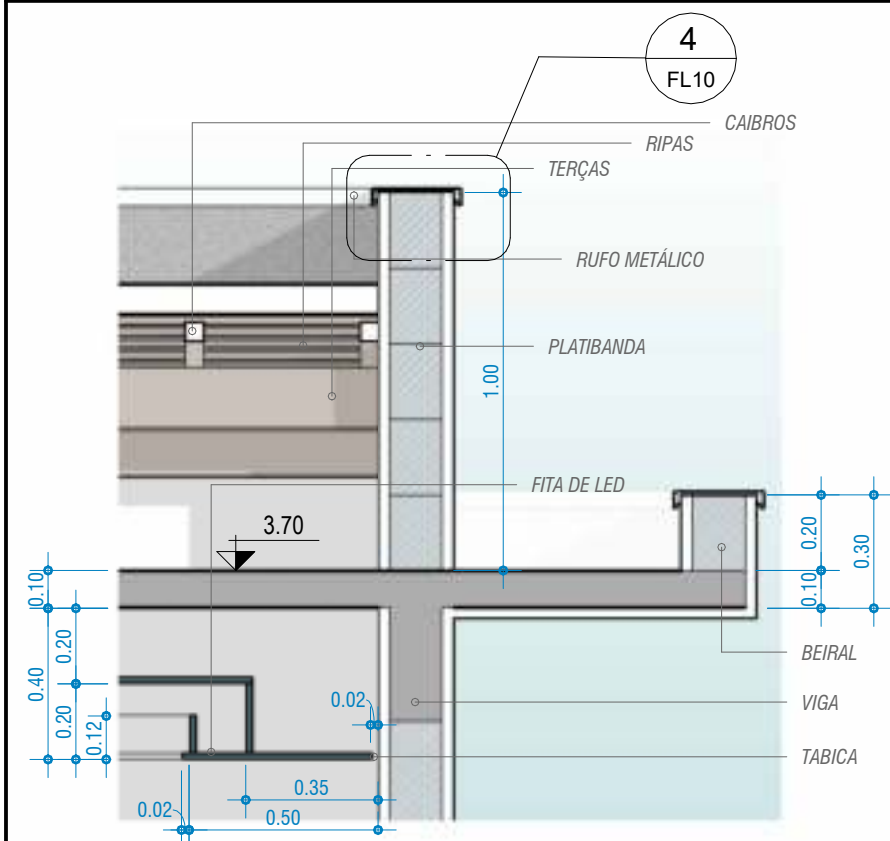


DET. 1 - CORTE 1. SANCA E PLATIBANDA

1 : 20

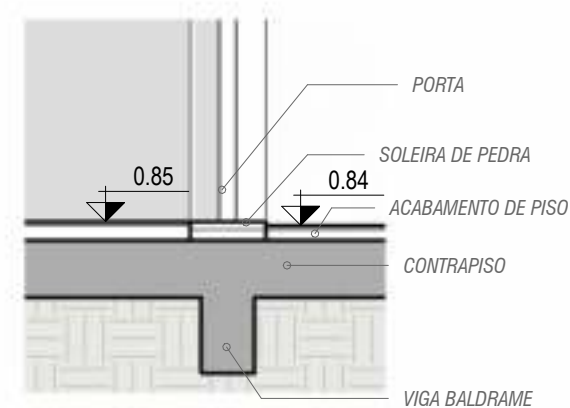


DET. 2 - CORTE 2. - SOLEIRAS

1 : 20

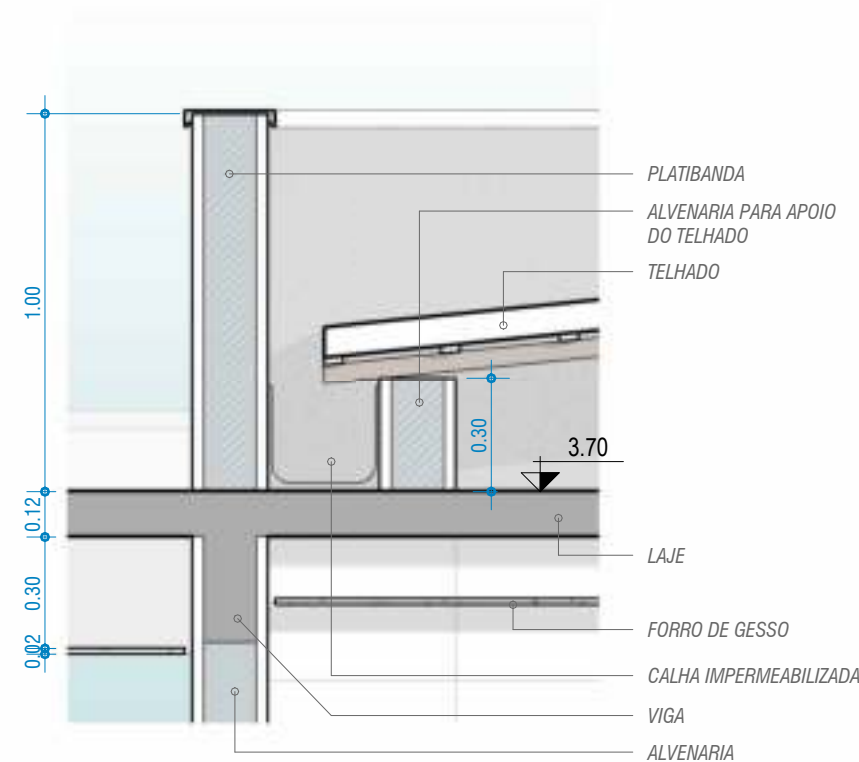


DET. 3 - CORTE 3. CALHA


1 : 20

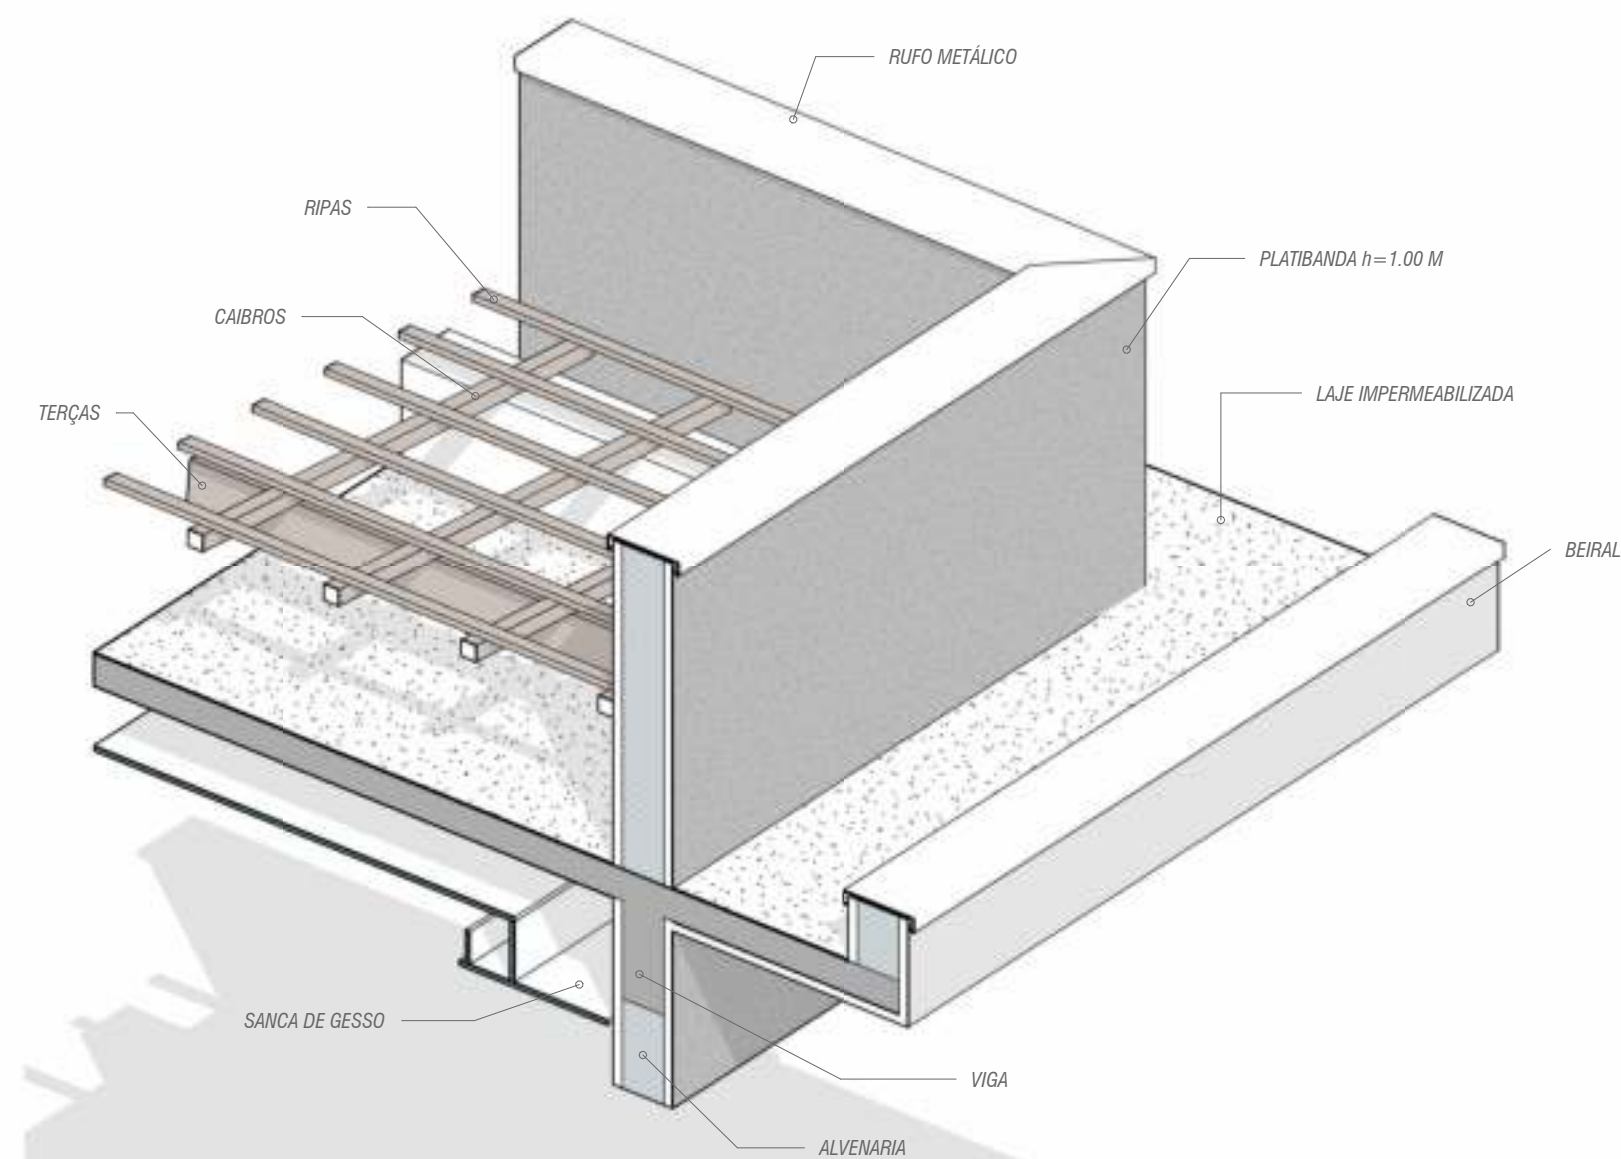

ISOMÉTRICO SANCA E PLATIBANDA

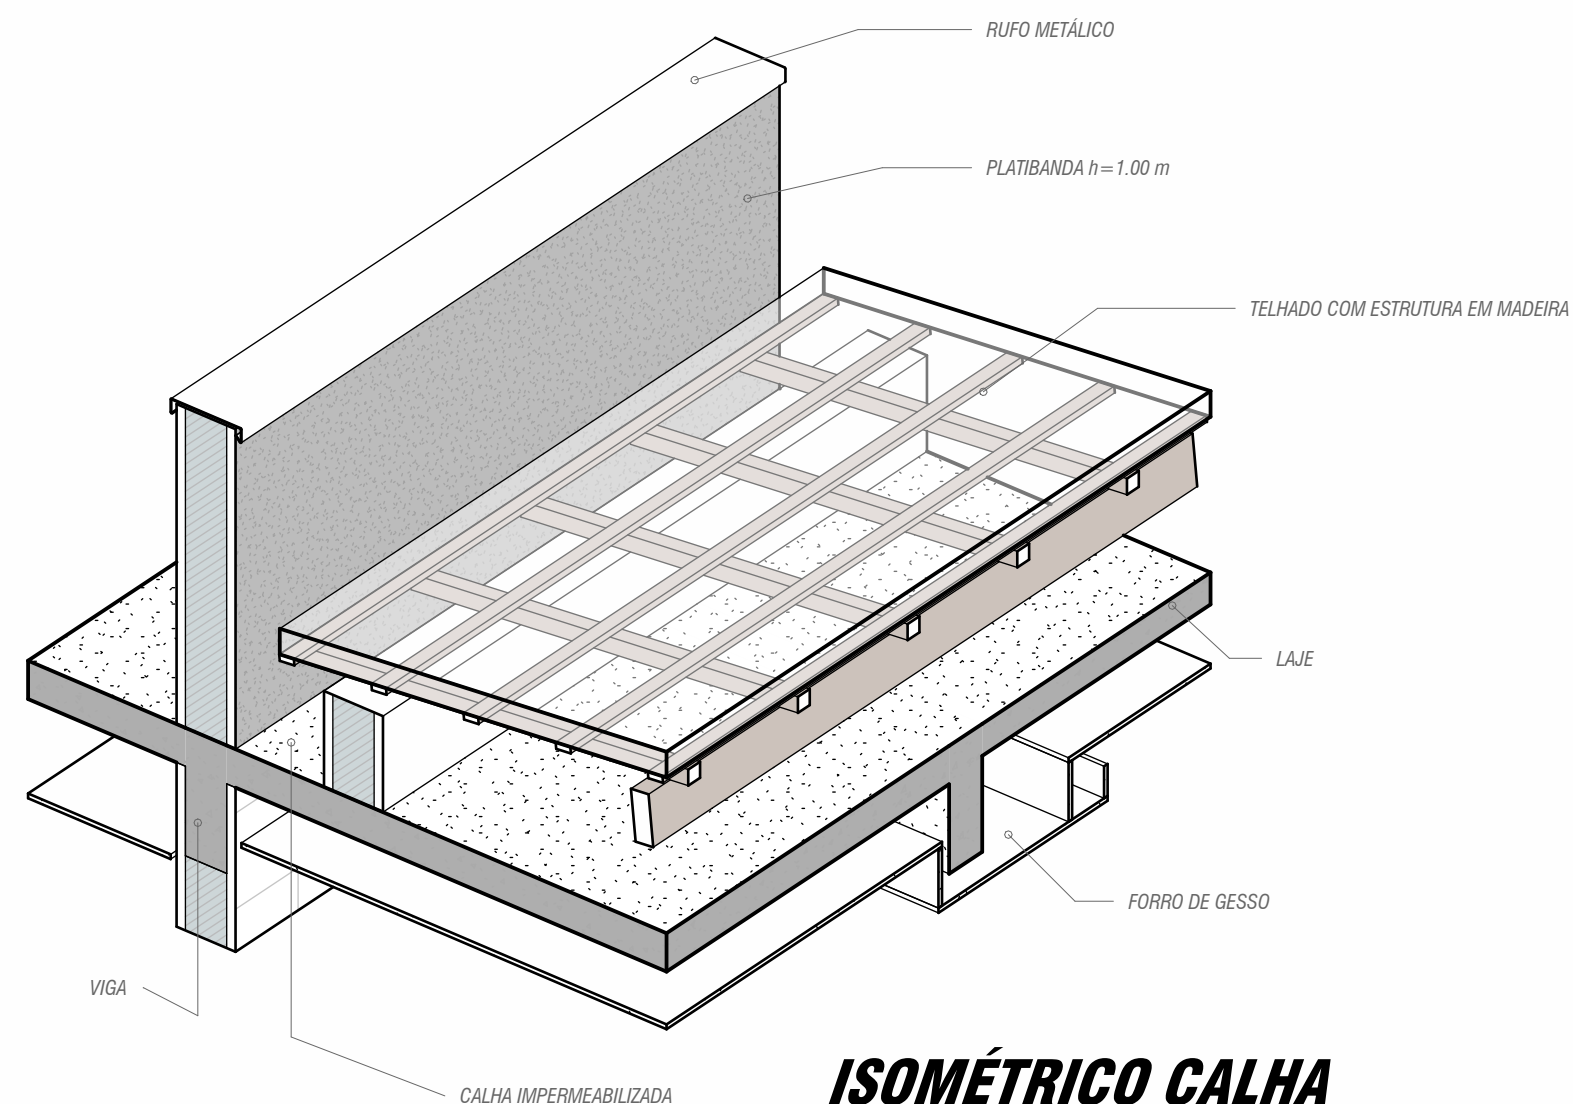


ISOMÉTRICO CALHA

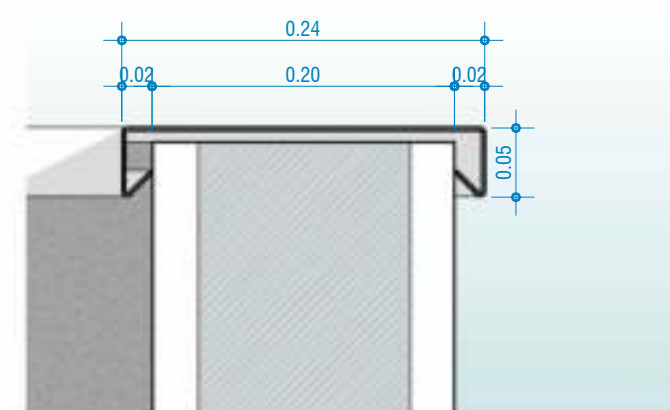


DET. 4 - CORTE 4. RUFO METÁLICO

1 : 5

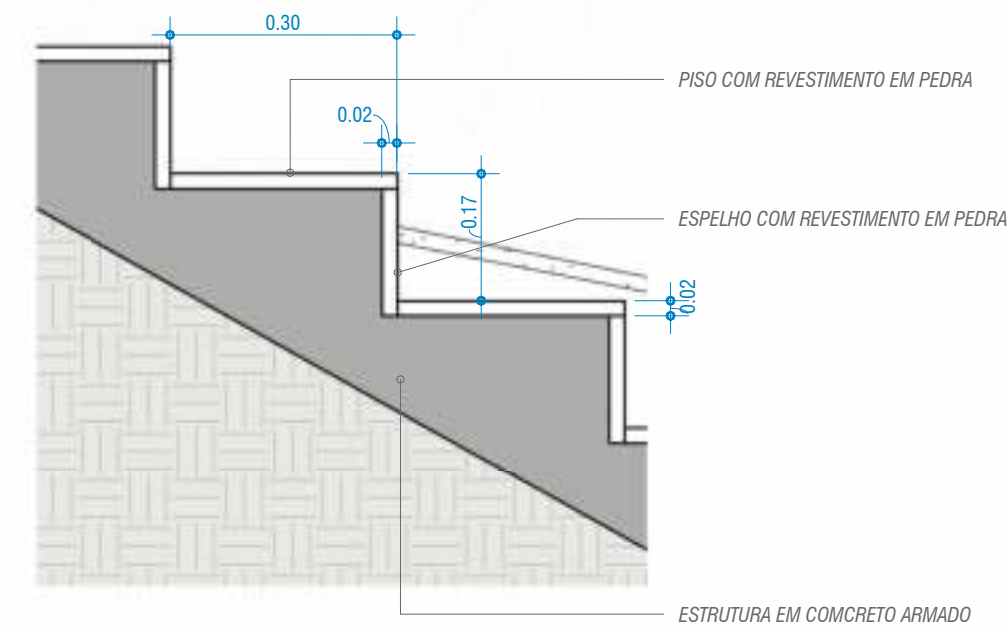

DET. 5 - CORTE 5. ESCADA

1 : 10

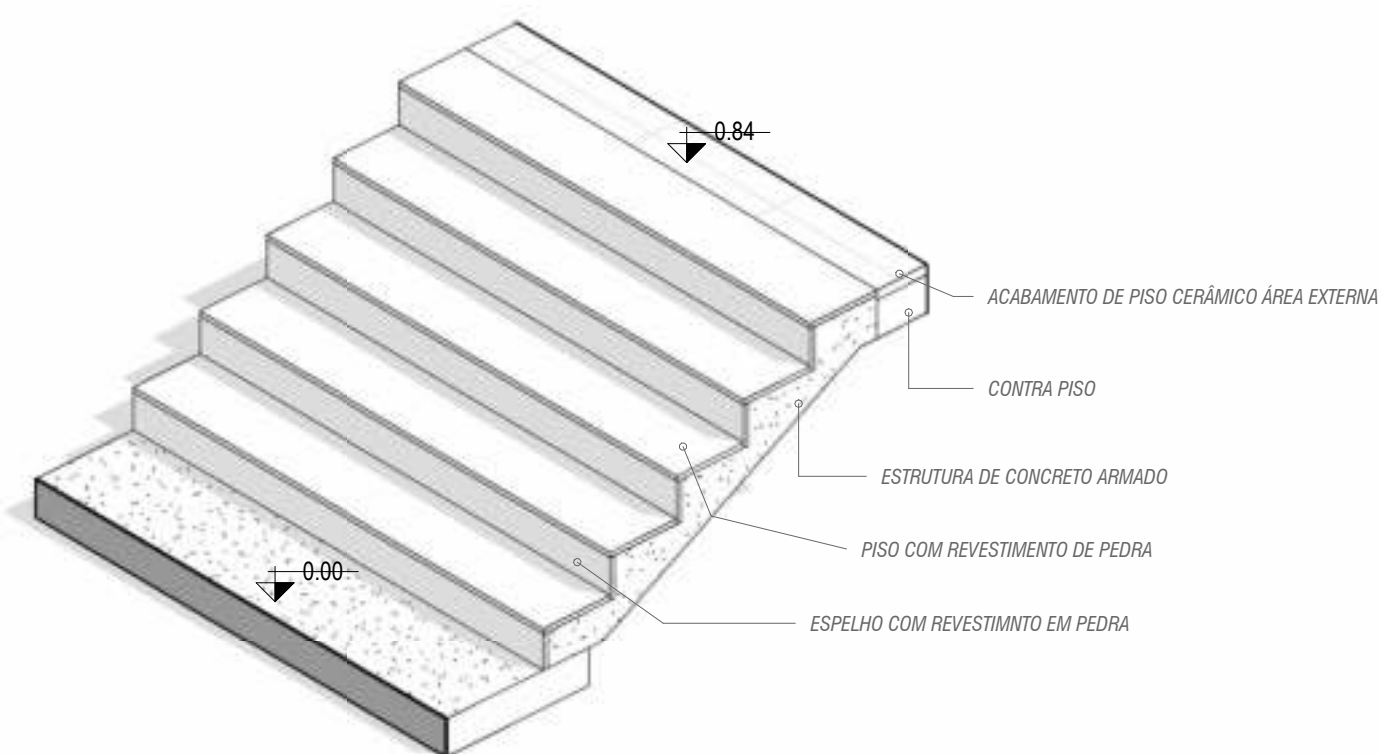

ISOMÉTRICO ESCADA

NATANAEL MENEZES DA SILVA

TELEFONE: (11) 95135-5191
LOCALIZAÇÃO: SÃO PAULO

INSTAGRAM: athenas.arq



CONCEITO DO PROJETO:
APRESENTAÇÃO DE PORTFÓLIO

NOME DO PROJETO:
RESIDÊNCIA ATHENAS
TIPO DE PROJETO:
PROJETO ARQUITETÔNICO

DESENHADOR POR:
Natanael Menezes da Silva

APROVADO POR:
Natanael Menezes da Silva

DATA:
01/05/23
ESCALA:
Como indicado

FOLHA:

FL10

FORMATO:
A2